
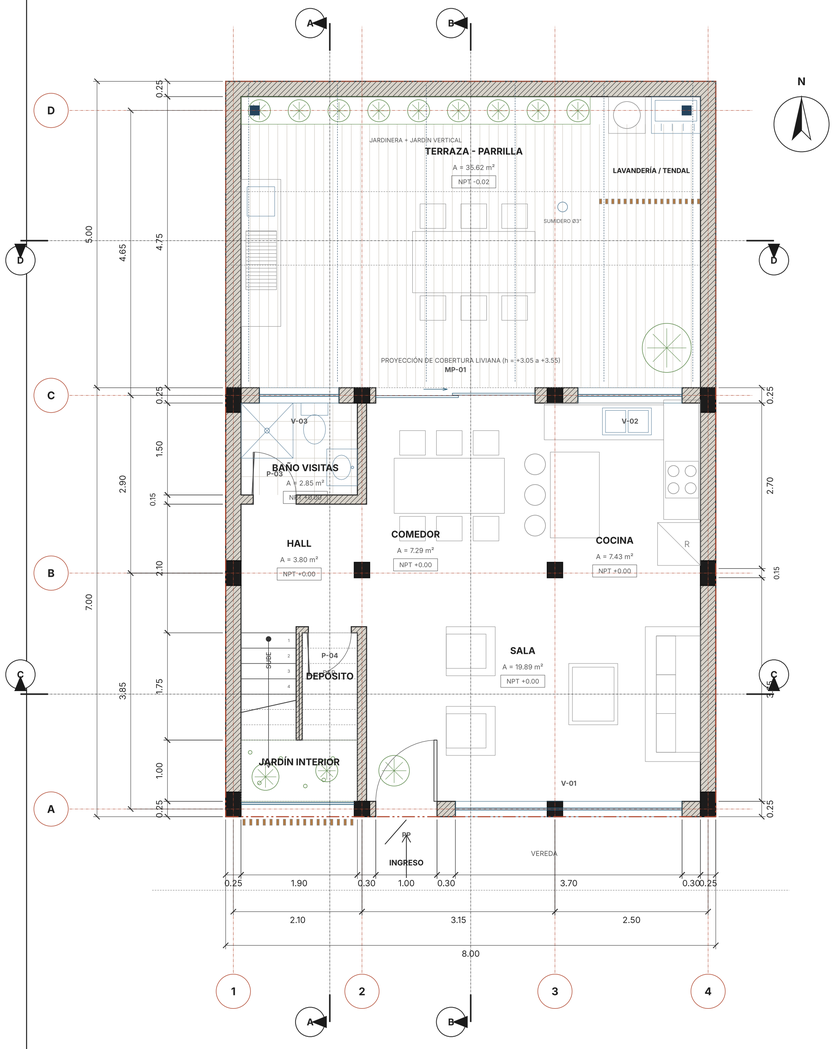


PLANTA 1er PISO — GENERAL

ESC. 1/50 · NPT ±0.00 | área libre 40.00 m²

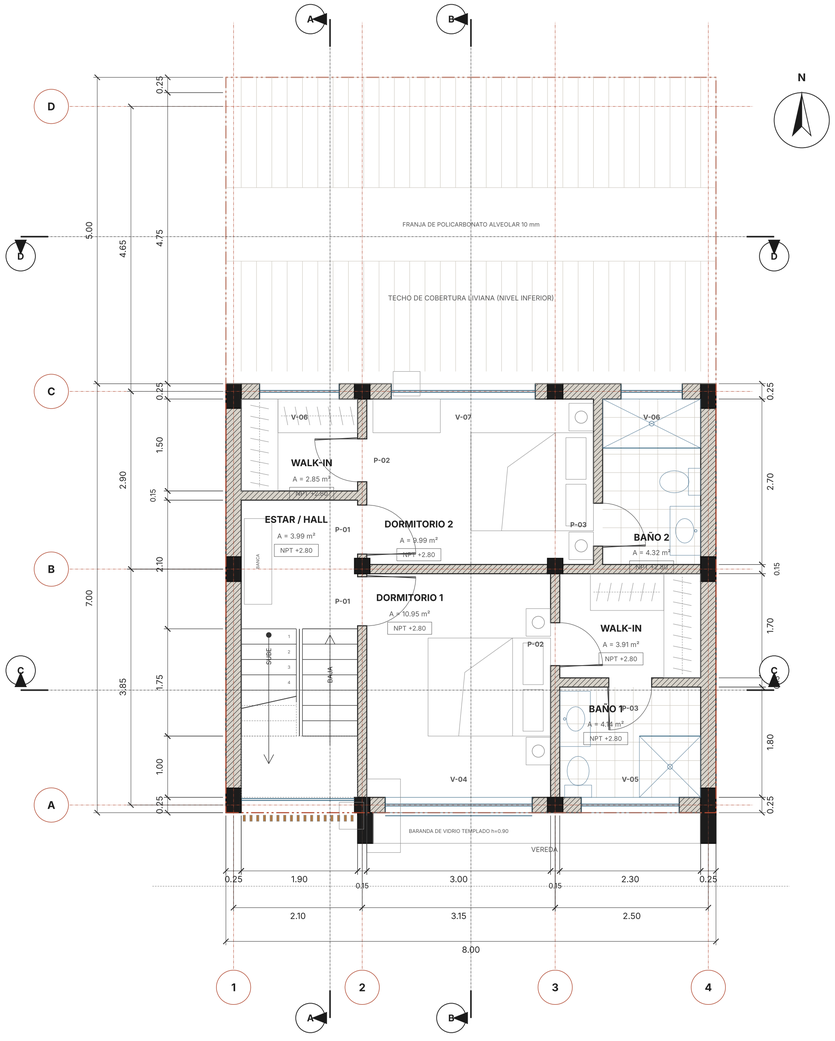

PLANTA 2do PISO

ESC. 1/50 · NPT +2.80 | 2 suites

CUADRO DE VANOS (cantidad Fase 1 + proyección)

CÓD.	TIPO	ANCHO	ALTO	ALF.	CANT.	DESCRIPCIÓN
P-01	PUERTA	0.80	2.10	0.00	2 (+2)	Dormitorio principal
P-02	PUERTA	0.70	2.10	0.00	2 (+2)	Walk-in closet
P-03	PUERTA	0.70	2.10	0.00	3 (+2)	Baño visitas
P-04	PUERTA	0.70	2.00	0.00	1	Depósito bajo escalera
P-05	PUERTA	0.80	2.10	0.00	0 (+1)	Salida a azotea
PP	PUERTA	1.00	2.40	0.00	1	Puerta principal pivotante de madera
MP-01	PUERTA	2.60	2.40	0.00	1	Mampara corrediza comedor-terraza
V-01	VENTANA	3.70	1.95	0.45	1	Ventanal sala
V-02	VENTANA	1.70	1.15	1.05	1	Ventana cocina
V-03	VENTANA	1.30	0.60	1.60	1	Ventana alta baño visitas
V-04	VENTANA	2.40	2.30	0.10	1 (+1)	Ventanal piso-techo + baranda vidrio
V-05	VENTANA	1.60	0.70	1.50	1 (+1)	Ventana alta baño
V-06	VENTANA	1.30	0.70	1.50	2 (+2)	Ventana walk-in
V-07	VENTANA	2.35	1.50	0.90	1 (+1)	Ventana dormitorio posterior

CUADRO DE AMBIENTES

NIV.	AMBIENTE	m²	ACABADO DE PISO
1°	SALA	19.89	Porcelanato 60×120
1°	COMEDOR	7.29	Porcelanato 60×120
1°	COCINA	7.43	Porcelanato 60×120
1°	HALL	3.80	Porcelanato 60×120
1°	BAÑO VISITAS	2.85	Cerámico antideslizante
1°	JARDÍN INTERIOR	1.90	Canto rodado + helechos
1°	DEPÓSITO	1.57	
1°	TERRAZA - PARRILLA	35.62	Porcelanato antideslizante / deck WPC
2°	DORMITORIO 1	10.95	Piso laminado
2°	WALK-IN	3.91	Piso laminado
2°	BAÑO 1	4.14	Porcelanato
2°	DORMITORIO 2	9.99	Piso laminado
2°	BAÑO 2	4.32	Porcelanato
2°	WALK-IN	2.85	Piso laminado
2°	ESTAR / HALL	3.99	Piso laminado
3°	DORMITORIO 3	10.95	Piso laminado
3°	WALK-IN	3.91	Piso laminado
3°	BAÑO 3	4.14	Porcelanato
3°	DORMITORIO 4	9.99	Piso laminado
3°	BAÑO 4	4.32	Porcelanato
3°	WALK-IN	2.85	Piso laminado
3°	ESTAR / HALL	3.99	Piso laminado

CASA LINTERNA

VIVIENDA UNIFAMILIAR · 2 PISOS + PROYECCIÓN 3er PISO

TERRENO
8.00 × 12.00 m = 96.00 m²

EDIFICACIÓN
8.00 × 7.00 m (material noble)

ÁREA LIBRE
8.00 × 5.00 m (cobertura liviana)

PROPIETARIO
_____

UBICACIÓN
_____

PROYECTISTA
_____

CAP / CIP N°
_____

ESPECIALIDAD
ARQUITECTURA

ÍNDICE DE LÁMINAS


A-01 PLANTAS 1er Y 2do PISO
A-02 PLANTA 3er PISO (PROYECCIÓN) Y TECHOS
A-03 CORTES LONGITUDINALES A-A Y B-B
A-04 CORTES TRANSVERSALES, COBERTURA Y DETALLES
A-05 ELEVACIONES
A-06 VISTAS 3D

LÁMINA
PLANTAS 1er Y 2do PISO

ESCALA
1/50


FECHA
OCTUBRE 2026

A-01

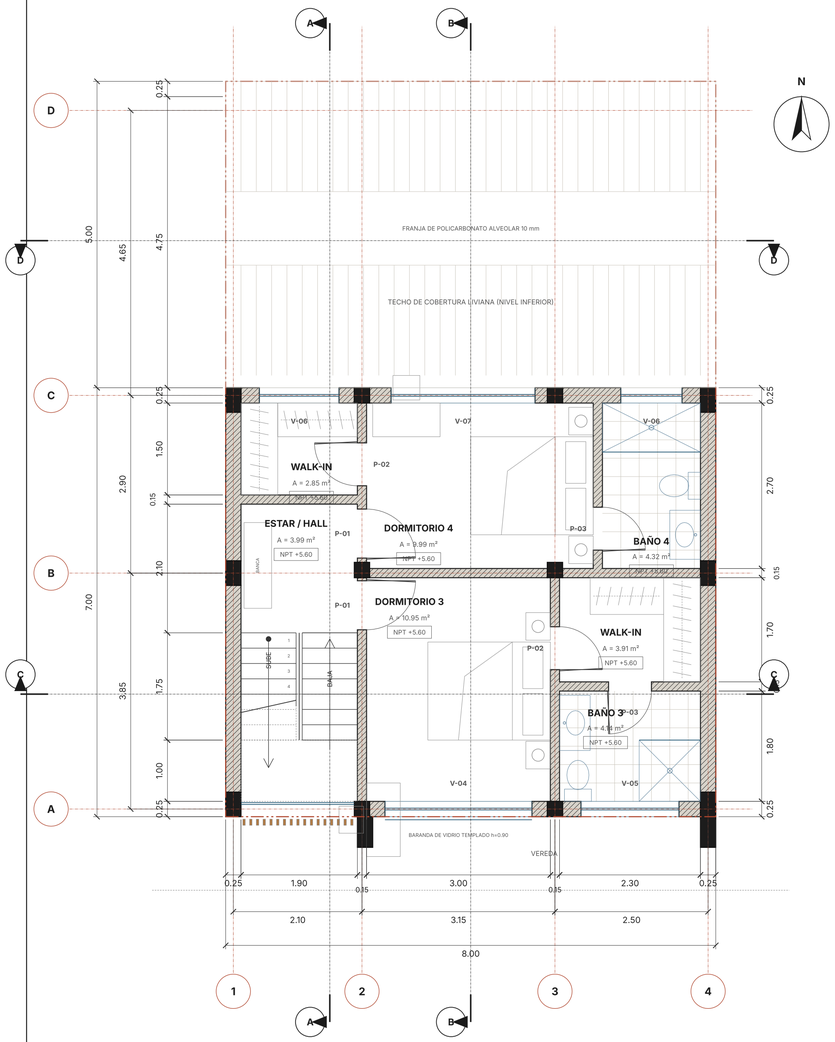

PLANTA 3er PISO — PROYECCIÓN (FASE 2)

ESC. 1/50 · NPT +5.60 | 2 suites

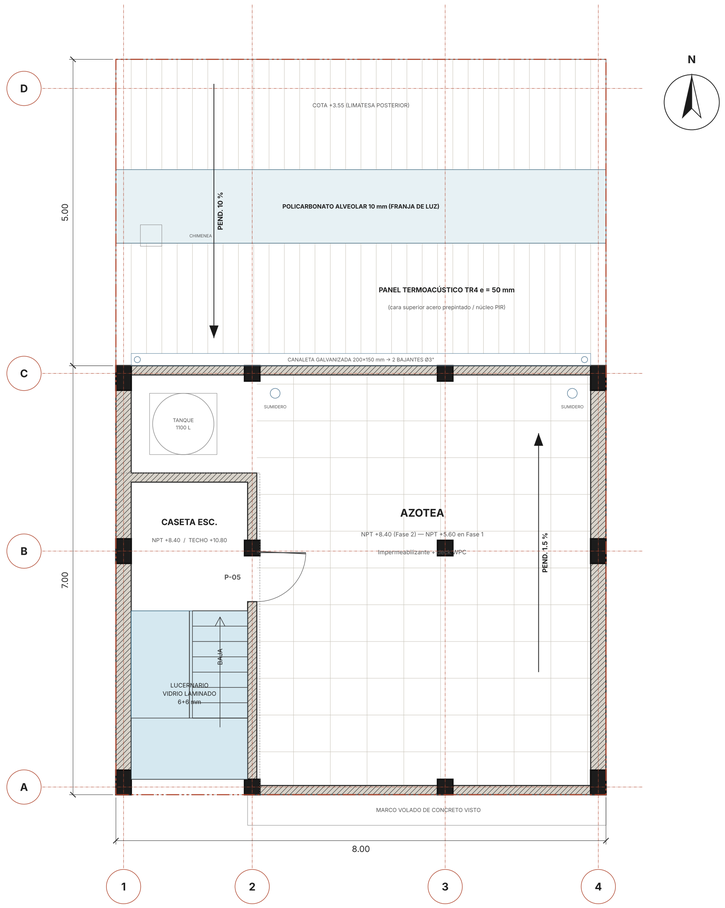

PLANTA DE TECHOS

ESC. 1/50 · azotea + cobertura liviana

CUADRO DE ÁREAS

ÍTEM	MEDIDAS (m)	ÁREA (m²)
TERRENO	8.00 × 12.00	96.00
ÁREA TECHADA 1er PISO	8.00 × 7.00	56.00
ÁREA TECHADA 2do PISO	8.00 × 7.00	56.00
SUBTOTAL FASE 1		**112.00**
ÁREA TECHADA 3er PISO (PROY.)	8.00 × 7.00	56.00
CASETA ESCALERA (PROY.)	2.30 × 5.25	12.08
TOTAL TECHADO (FASE 1 + 2)		**180.08**
ÁREA LIBRE (cob. liviana)	8.00 × 5.00	40.00 (41.7 %)

LEYENDA

- Muro de albañilería (ladrillo KK 18 huecos)
- Columna / placa de concreto armado
- Proyección superior / elemento oculto
- Estructura metálica (tubo LAC ASTM A500)
- Eje estructural
- Vidrio / policarbonato

NOTAS GENERALES

1. Cotas y niveles en metros; verificar en obra antes de ejecutar.
2. Muros: albañilería confinada de ladrillo KK; tarrajeo frotachado e=1.5 cm.
3. Losas aligeradas h=0.20 m; vigas 0.25×0.40 m; columnas C-1 0.25×0.40, C-2 0.25×0.25.
4. Estructura referencial: requiere diseño por Ing. Civil colegiado (E.030, E.060, E.070, E.090).
5. El 3er piso es PROYECCIÓN (Fase 2): columnas y cimentación dimensionadas para 3 niveles.
6. Área libre cubierta con cobertura liviana desmontable (sin cerramiento lateral).
7. Baños sin ventana exterior directa ventilan por ducto/extractor a azotea.
8. Escalera: contrapaso 0.175, paso 0.25, ancho libre 0.90 m por tramo.

CASA LINTERNA

VIVIENDA UNIFAMILIAR · 2 PISOS + PROYECCIÓN 3er PISO

TERRENO
8.00 × 12.00 m = 96.00 m²

EDIFICACIÓN
8.00 × 7.00 m (material noble)

ÁREA LIBRE
8.00 × 5.00 m (cobertura liviana)

PROPIETARIO
_____

UBICACIÓN
_____

PROYECTISTA
_____

CAP / CIP N°
_____

ESPECIALIDAD
ARQUITECTURA

ÍNDICE DE LÁMINAS


A-01 PLANTAS 1er Y 2do PISO
A-02 PLANTA 3er PISO (PROYECCIÓN) Y TECHOS
A-03 CORTES LONGITUDINALES A-A Y B-B
A-04 CORTES TRANSVERSALES, COBERTURA Y DETALLES
A-05 ELEVACIONES
A-06 VISTAS 3D

LÁMINA
PLANTA 3er PISO (PROYECCIÓN) Y TECHOS

ESCALA
1/50


FECHA
OCTUBRE 2026

A-02

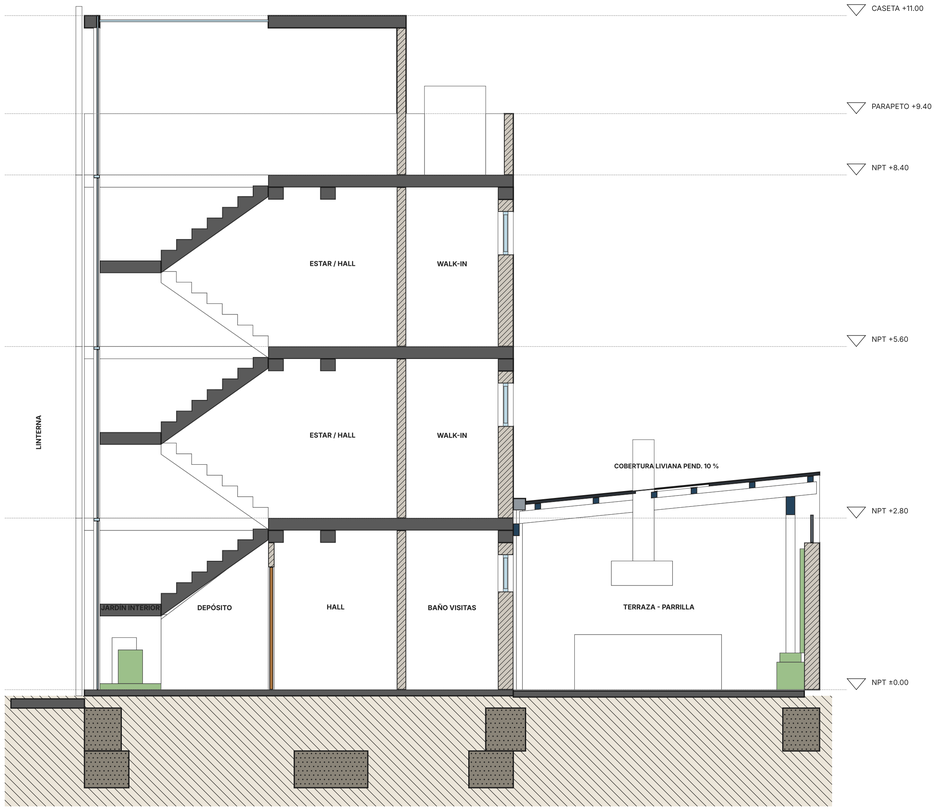

CORTE A-A

ESC. 1/50 · por escalera — linterna

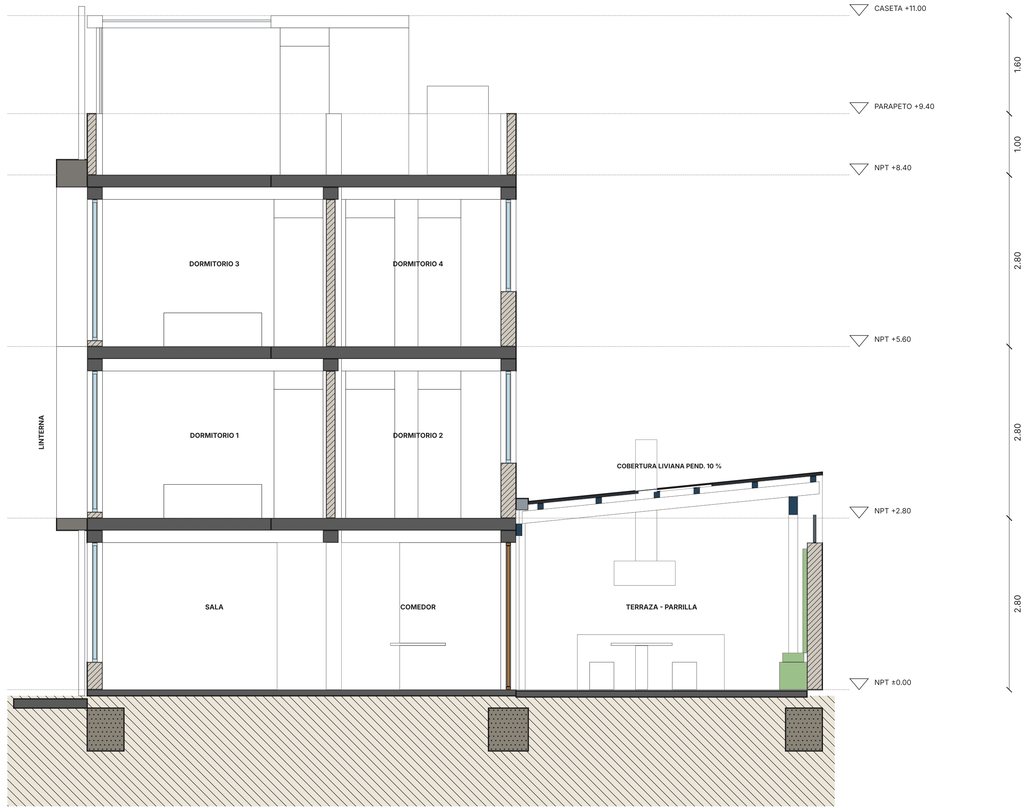

CORTE B-B

ESC. 1/50 · por sala, dormitorios y área libre

CASA LINTERNA

VIVIENDA UNIFAMILIAR · 2 PISOS + PROYECCIÓN 3er PISO

TERRENO
8.00 × 12.00 m = 96.00 m²

EDIFICACIÓN
8.00 × 7.00 m (material noble)

ÁREA LIBRE
8.00 × 5.00 m (cobertura liviana)

PROPIETARIO
_____

UBICACIÓN
_____

PROYECTISTA
_____

CAP / CIP N°
_____

ESPECIALIDAD
ARQUITECTURA

ÍNDICE DE LÁMINAS


A-01 PLANTAS 1er Y 2do PISO
A-02 PLANTA 3er PISO (PROYECCIÓN) Y TECHOS
A-03 CORTES LONGITUDINALES A-A Y B-B
A-04 CORTES TRANSVERSALES, COBERTURA Y DETALLES
A-05 ELEVACIONES
A-06 VISTAS 3D

LÁMINA
CORTES LONGITUDINALES A-A Y B-B

ESCALA
1/50


FECHA
OCTUBRE 2026

A-03

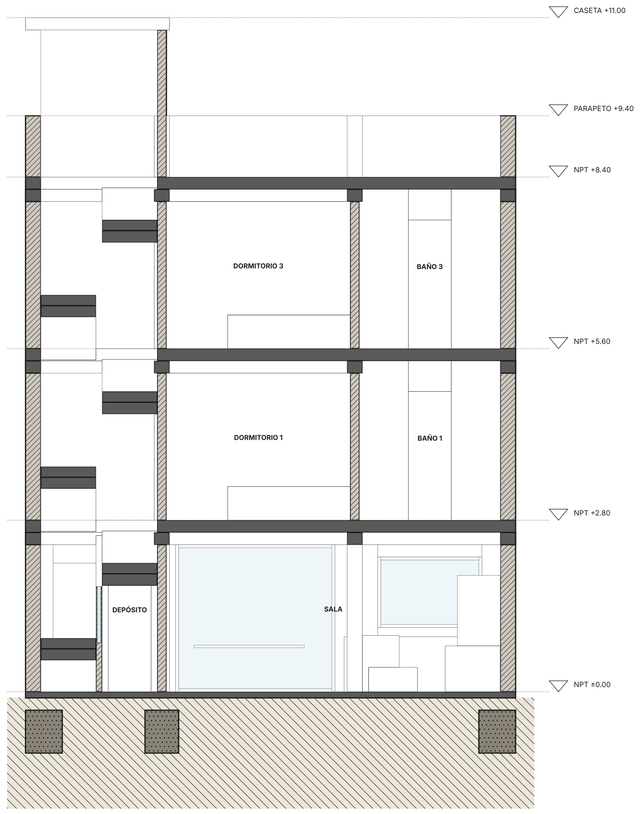


CORTE C-C

ESC. 1/50 · por escalera y dormitorios frontales

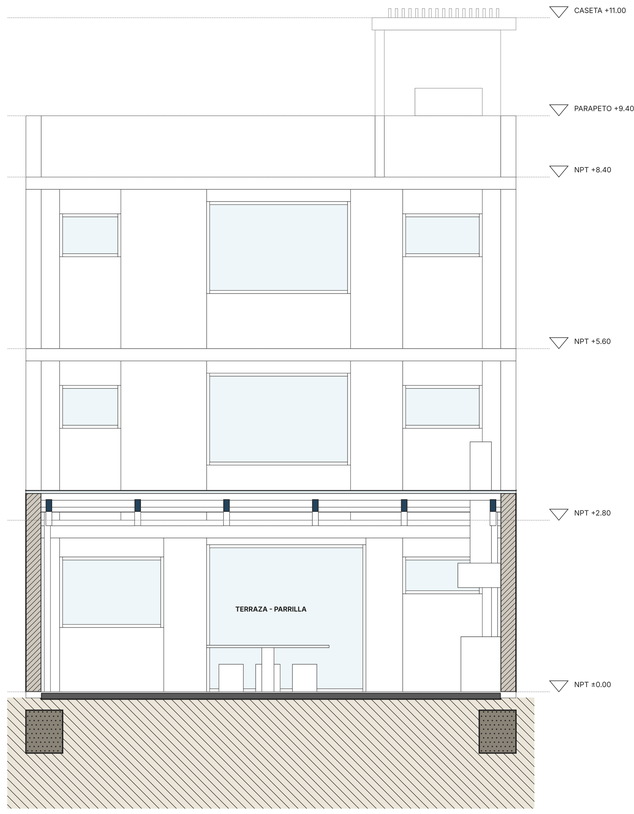

CORTE D-D

ESC. 1/50 · por área libre, mirando a la fachada posterior

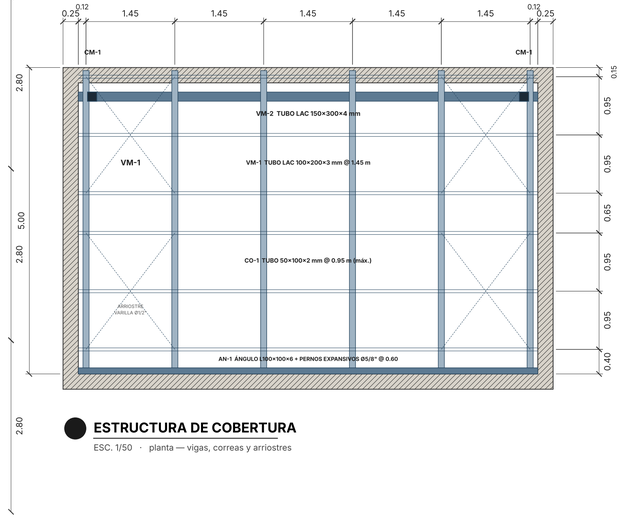


ESTRUCTURA DE COBERTURA

ESC. 1/50 · planta — vigas, correas y arriostres


CUADRO DE ELEMENTOS METÁLICOS — COBERTURA

CÓD.	ELEMENTO	SECCIÓN / ESPECIFICACIÓN	CANT.
CM-1	Columna	Tubo LAC 150×150×4 mm	2
VM-1	Viga principal	Tubo LAC 100×200×3 mm @1.45	6
VM-2	Viga posterior	Tubo LAC 150×300×4 mm	1
CO-1	Correa	Tubo LAC 50×100×2 mm @0.95	6
AN-1	Apoyo en edificio	Ángulo L100×100×6 + pernos Ø5/8"	1
AR-1	Arriostre	Varilla lisa Ø1/2" con templador	8
PL-1	Placa base	PL 300×300×12 + 4 pernos Ø5/8" L=0.40	2
CB-1	Cobertura	Panel TR4 termoacústico e=50 mm	33 m²
CB-2	Franja de luz	Policarbonato alveolar 10 mm UV	9.6 m²
CA-1	Canaleta + bajantes	Plancha galv. e=0.9 mm + 2 Ø3" PVC	1
—	Acabado	Anticorrosivo epóxico + esmalte poliuretano grafito	

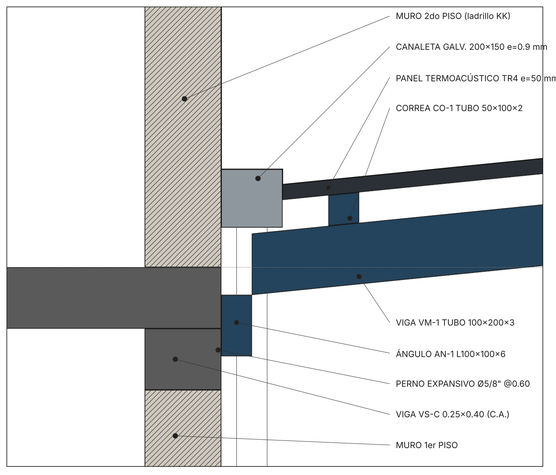

DETALLE 1 — APOYO EN EDIFICIO

ESC. 1/10 · corte por viga VM-1

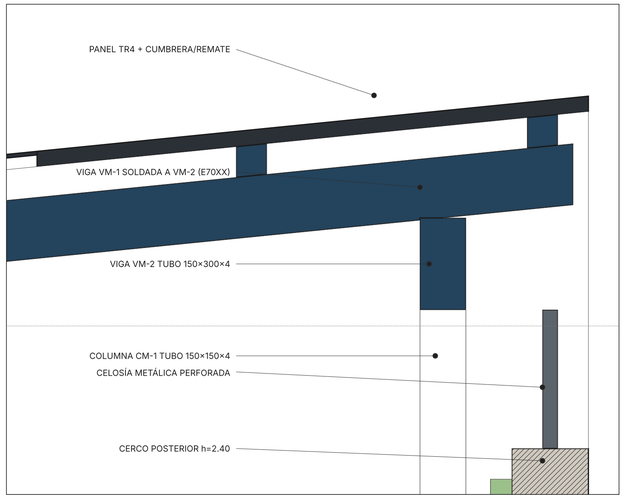

DETALLE 2 — APOYO POSTERIOR

ESC. 1/10 · viga VM-2 sobre columna CM-1

CASA LINTERNA

VIVIENDA UNIFAMILIAR · 2 PISOS + PROYECCIÓN 3er PISO

TERRENO
8.00 × 12.00 m = 96.00 m²

EDIFICACIÓN
8.00 × 7.00 m (material noble)

ÁREA LIBRE
8.00 × 5.00 m (cobertura liviana)

PROPIETARIO
_____

UBICACIÓN
_____

PROYECTISTA
_____

CAP / CIP N°
_____

ESPECIALIDAD
ARQUITECTURA

ÍNDICE DE LÁMINAS


A-01 PLANTAS 1er Y 2do PISO
A-02 PLANTA 3er PISO (PROYECCIÓN) Y TECHOS
A-03 CORTES LONGITUDINALES A-A Y B-B
A-04 CORTES TRANSVERSALES, COBERTURA Y DETALLES
A-05 ELEVACIONES
A-06 VISTAS 3D

LÁMINA
CORTES TRANSVERSALES, COBERTURA Y DETALLES

ESCALA
INDICADA


FECHA
OCTUBRE 2026

A-04

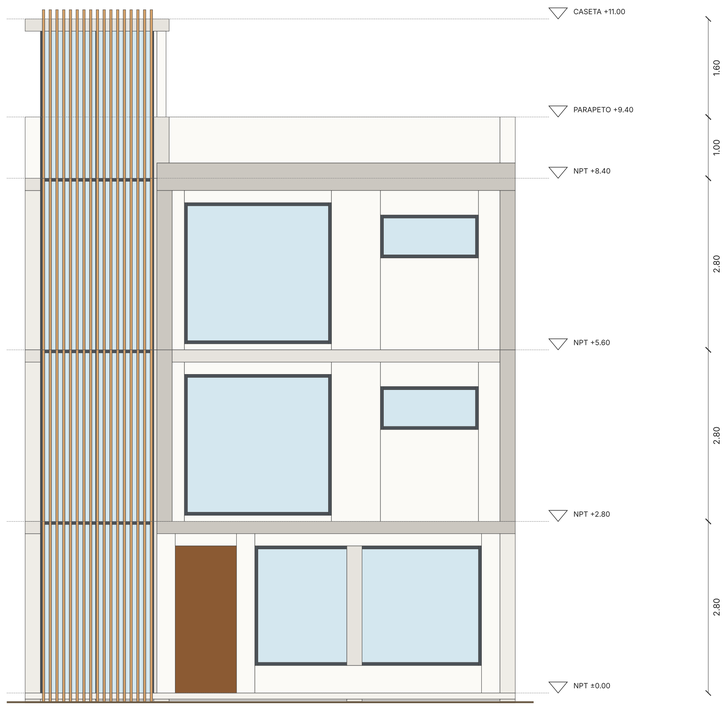

ELEVACIÓN PRINCIPAL (CALLE)

ESC. 1/50 · marco volado de concreto visto + linterna de celosía

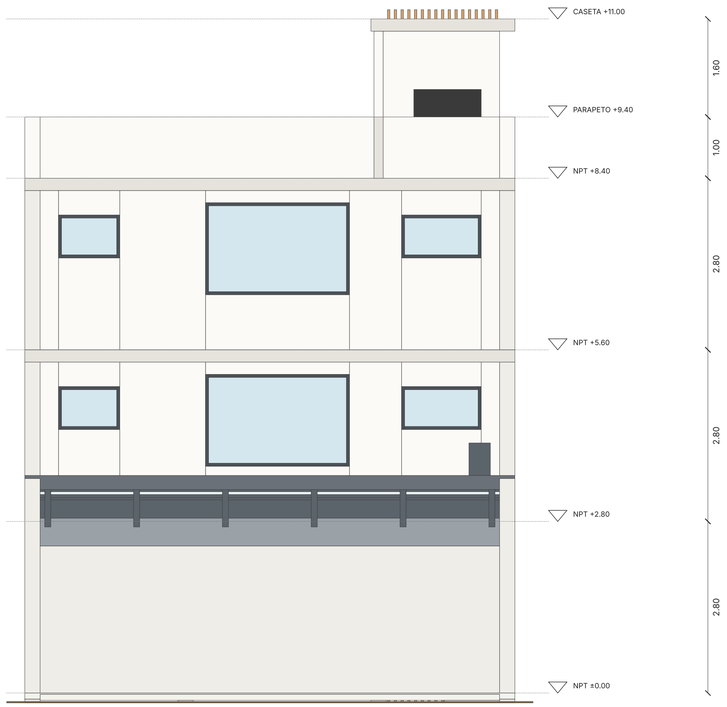


ELEVACIÓN POSTERIOR

ESC. 1/50 · hacia el área libre (cobertura en primer plano)



VISTA DESDE LA CALLE

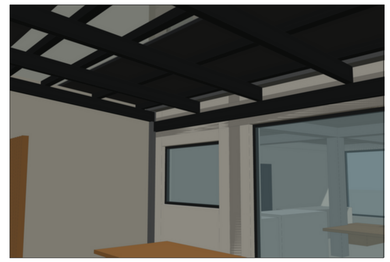

ÁREA LIBRE CON COBERTURA LIVIANA

CASA LINTERNA

VIVIENDA UNIFAMILIAR · 2 PISOS + PROYECCIÓN 3er PISO

TERRENO
8.00 × 12.00 m = 96.00 m²

EDIFICACIÓN
8.00 × 7.00 m (material noble)

ÁREA LIBRE
8.00 × 5.00 m (cobertura liviana)

PROPIETARIO
_____

UBICACIÓN
_____

PROYECTISTA
_____

CAP / CIP N°
_____

ESPECIALIDAD
ARQUITECTURA

ÍNDICE DE LÁMINAS

A-01 PLANTAS 1er Y 2do PISO
A-02 PLANTA 3er PISO (PROYECCIÓN) Y TECHOS
A-03 CORTES LONGITUDINALES A-A Y B-B
A-04 CORTES TRANSVERSALES, COBERTURA Y DETALLES
A-05 ELEVACIONES
A-06 VISTAS 3D

LÁMINA
ELEVACIONES

ESCALA
1/50

FECHA
OCTUBRE 2026


A-05




ISOMÉTRICA GENERAL



CORTE FUGADO LONGITUDINAL

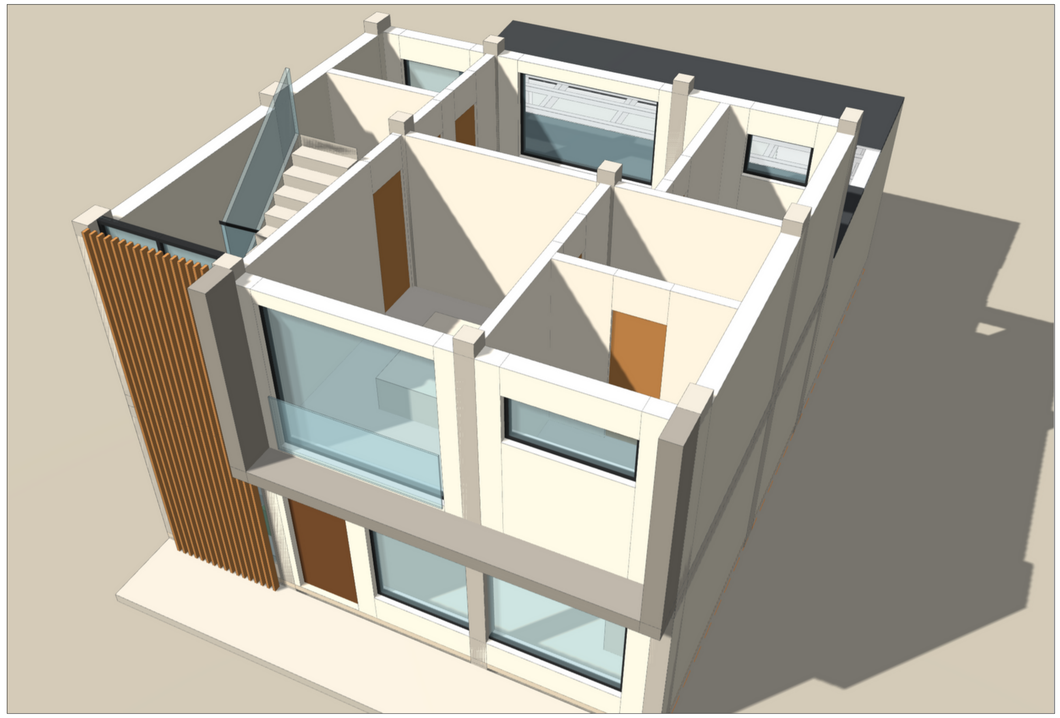

2do PISO — DISTRIBUCIÓN DE SUITES

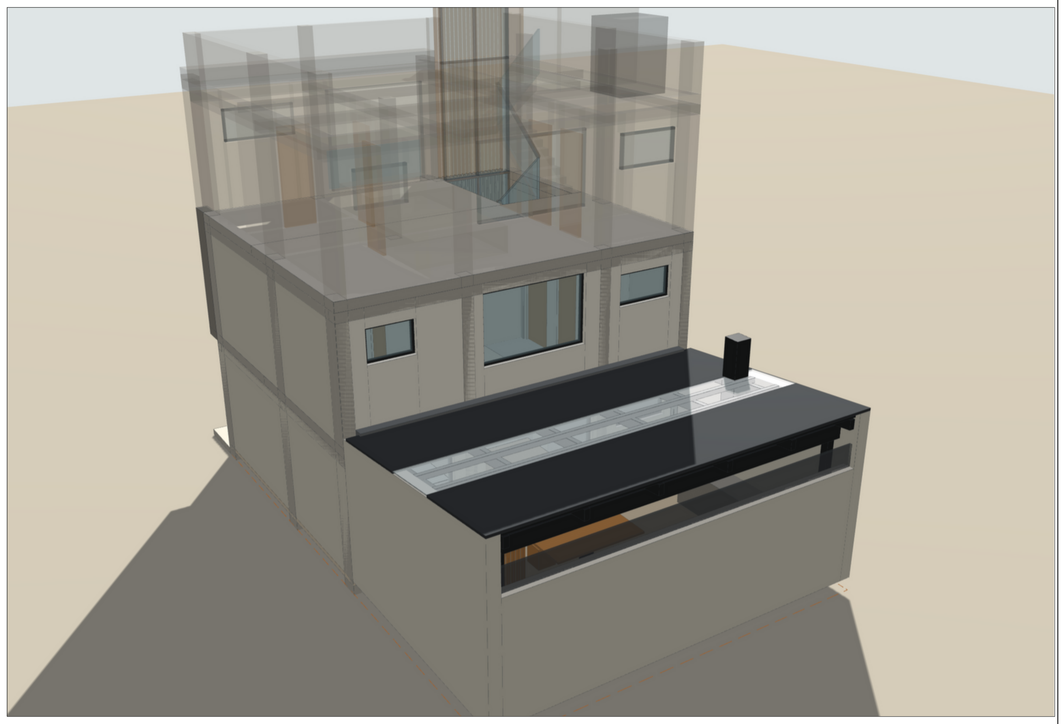

VISTA POSTERIOR (3er PISO EN FANTASMA)

CASA LINTERNA

VIVIENDA UNIFAMILIAR · 2 PISOS + PROYECCIÓN 3er PISO

TERRENO
8.00 × 12.00 m = 96.00 m²

EDIFICACIÓN
8.00 × 7.00 m (material noble)

ÁREA LIBRE
8.00 × 5.00 m (cobertura liviana)

PROPIETARIO
_____

UBICACIÓN
_____

PROYECTISTA
_____

CAP / CIP N°
_____

ESPECIALIDAD
ARQUITECTURA

ÍNDICE DE LÁMINAS

A-01 PLANTAS 1er Y 2do PISO
A-02 PLANTA 3er PISO (PROYECCIÓN) Y TECHOS
A-03 CORTES LONGITUDINALES A-A Y B-B
A-04 CORTES TRANSVERSALES, COBERTURA Y DETALLES
A-05 ELEVACIONES
A-06 VISTAS 3D

LÁMINA
VISTAS 3D

ESCALA
S/E

FECHA
OCTUBRE 2026

A-06