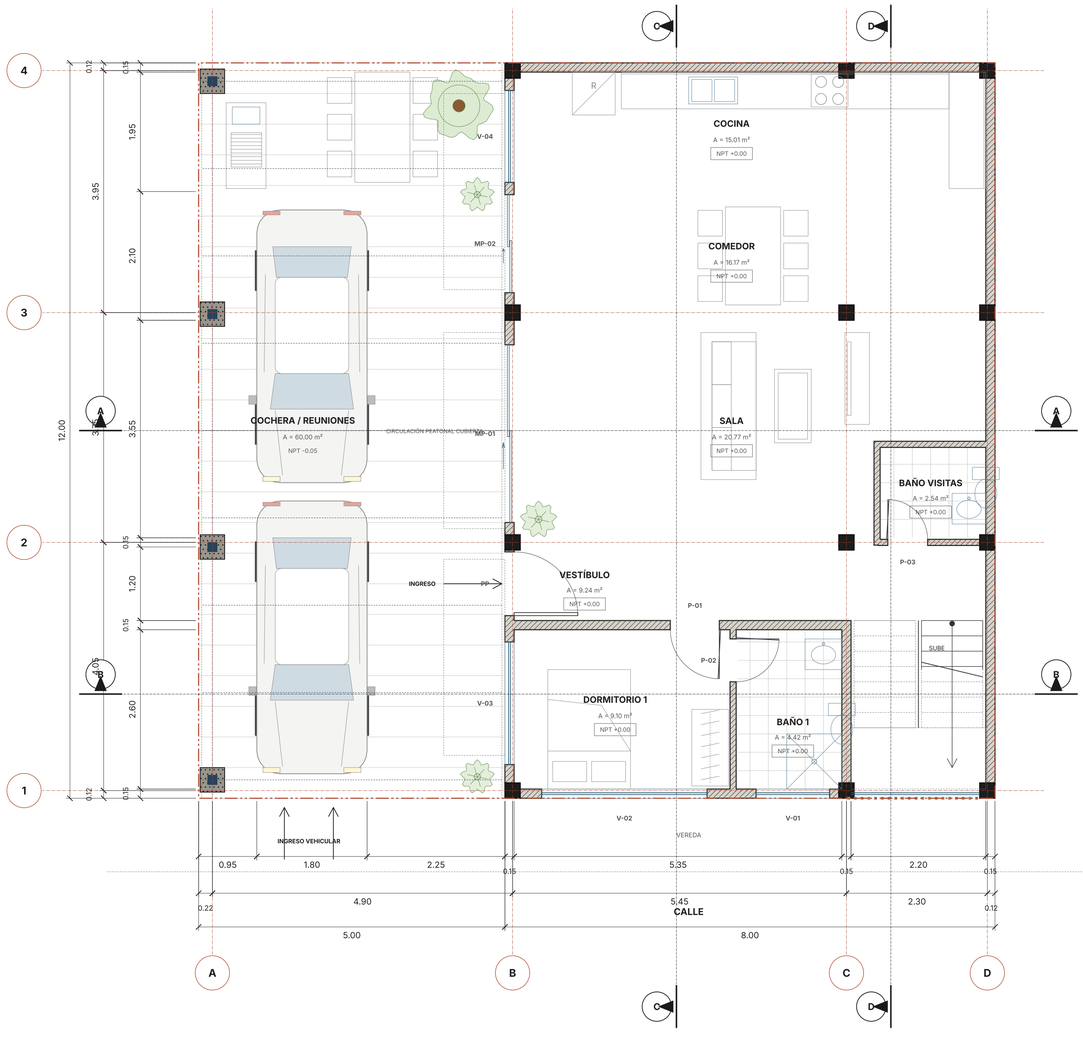


PLANTA 1er PISO — GENERAL

ESC. 1/50 · NPT ±0.00 | sala, comedor, cocina, dormitorio + franja techada

CUADRO DE VANOS

CÓD.	TIPO	ANCHO	ALTO	ALF.	CANT.	DESCRIPCIÓN
P-01	PUERTA	0.80	2.10	0.00	4	Dormitorio 1er piso
P-02	PUERTA	0.70	2.10	0.00	4	Baño dormitorio
P-03	PUERTA	0.65	2.10	0.00	1	Baño de visitas
PP	PUERTA	1.04	2.40	0.00	1	Puerta principal pivotante de madera
MP-01	PUERTA	2.90	2.40	0.00	1	Mampara corrediza sala-franja
MP-02	PUERTA	1.60	2.40	0.00	1	Mampara corrediza comedor-franja
MP-03	PUERTA	2.60	2.40	0.00	3	Mampara corrediza a balcón
V-01	VENTANA	1.20	0.60	1.60	2	Ventana alta baño (calle)
V-02	VENTANA	2.70	1.50	0.90	2	Ventana dormitorio (calle)
V-03	VENTANA	2.00	1.50	0.90	1	Ventana dormitorio a la franja
V-04	VENTANA	1.50	1.15	1.05	1	Ventana cocina

CASA LINTERNA

VIVIENDA UNIFAMILIAR · 2 PISOS + TERRAZA + FRANJA TECHADA

TERRENO
13.00 × 12.00 m = 156.00 m²

VIVIENDA
8.00 × 12.00 m · 2 pisos (material noble)

FRANJA LIBRE
5.00 × 12.00 m · cochera (cob. liviana)

PROPIETARIO
_____

UBICACIÓN
_____

PROYECTISTA
_____

CAP / CIP N°
_____

ESPECIALIDAD
ARQUITECTURA

ÍNDICE DE LÁMINAS

A-01 PLANTA 1er PISO
A-02 PLANTA 2do PISO
A-03 PLANTA DE TERRAZA
A-04 TECHOS, ESTRUCTURA METÁLICA Y DETALLES
A-05 CORTES TRANSVERSALES A-A Y B-B
A-06 CORTES LONGITUDINALES C-C Y D-D
A-07 ELEVACIONES
A-08 VISTAS 3D

LÁMINA
PLANTA 1er PISO

ESCALA
1/50

FECHA
OCTUBRE 2026

A-01



PLANTA 2do PISO

ESC. 1/50 · NPT +2.80 | 3 dormitorios con baño y balcón

CUADRO DE AMBIENTES

NIV.	AMBIENTE	m²	ACABADO DE PISO
1°	COCHERA / REUNIONES	60.00	Concreto estampado
1°	DORMITORIO 1	9.10	Piso laminado
1°	BAÑO 1	4.42	Porcelanato
1°	VESTÍBULO	9.24	Porcelanato 60×120
1°	BAÑO VISITAS	2.54	Cerámico
1°	SALA	20.77	Porcelanato 60×120
1°	COMEDOR	16.17	Porcelanato 60×120
1°	COCINA	15.01	Porcelanato 60×120
2°	DORMITORIO 2	17.99	Piso laminado
2°	BAÑO 2	2.88	Porcelanato
2°	DORMITORIO 3	16.56	Piso laminado
2°	BAÑO 3	4.43	Porcelanato
2°	DORMITORIO 4	20.60	Piso laminado
2°	BAÑO 4	4.73	Porcelanato
2°	WALK-IN	3.62	Piso laminado
2°	HALL	6.39	Piso laminado
3°	TERRAZA	84.04	Porcelanato antideslizante

CUADRO DE ÁREAS

ÍTEM	MEDIDAS (m)	ÁREA (m²)
TERRENO	13.00 × 12.00	156.00
ÁREA TECHADA 1er PISO	8.00 × 12.00	96.00
ÁREA TECHADA 2do PISO	8.00 × 12.00	96.00
BALCONES (volados)	3 × 3.20 × 1.00	9.60
TOTAL MATERIAL NOBLE		**192.00**
TERRAZA (cobertura liviana)	8.00 × 12.00	96.00
FRANJA LIBRE (cobertura liviana)	5.00 × 12.00	60.00 (38.5 %)

CASA LINTERNA

VIVIENDA UNIFAMILIAR · 2 PISOS + TERRAZA + FRANJA TECHADA

TERRENO
13.00 × 12.00 m = 156.00 m²

VIVIENDA
8.00 × 12.00 m · 2 pisos (material noble)

FRANJA LIBRE
5.00 × 12.00 m · cochera (cob. liviana)

PROPIETARIO
_____

UBICACIÓN
_____

PROYECTISTA
_____

CAP / CIP N°
_____

ESPECIALIDAD
ARQUITECTURA

ÍNDICE DE LÁMINAS


A-01 PLANTA 1er PISO
A-02 PLANTA 2do PISO
A-03 PLANTA DE TERRAZA
A-04 TECHOS, ESTRUCTURA METÁLICA Y DETALLES
A-05 CORTES TRANSVERSALES A-A Y B-B
A-06 CORTES LONGITUDINALES C-C Y D-D
A-07 ELEVACIONES
A-08 VISTAS 3D

LÁMINA
PLANTA 2do PISO

ESCALA
1/50

FECHA
OCTUBRE 2026

A-02

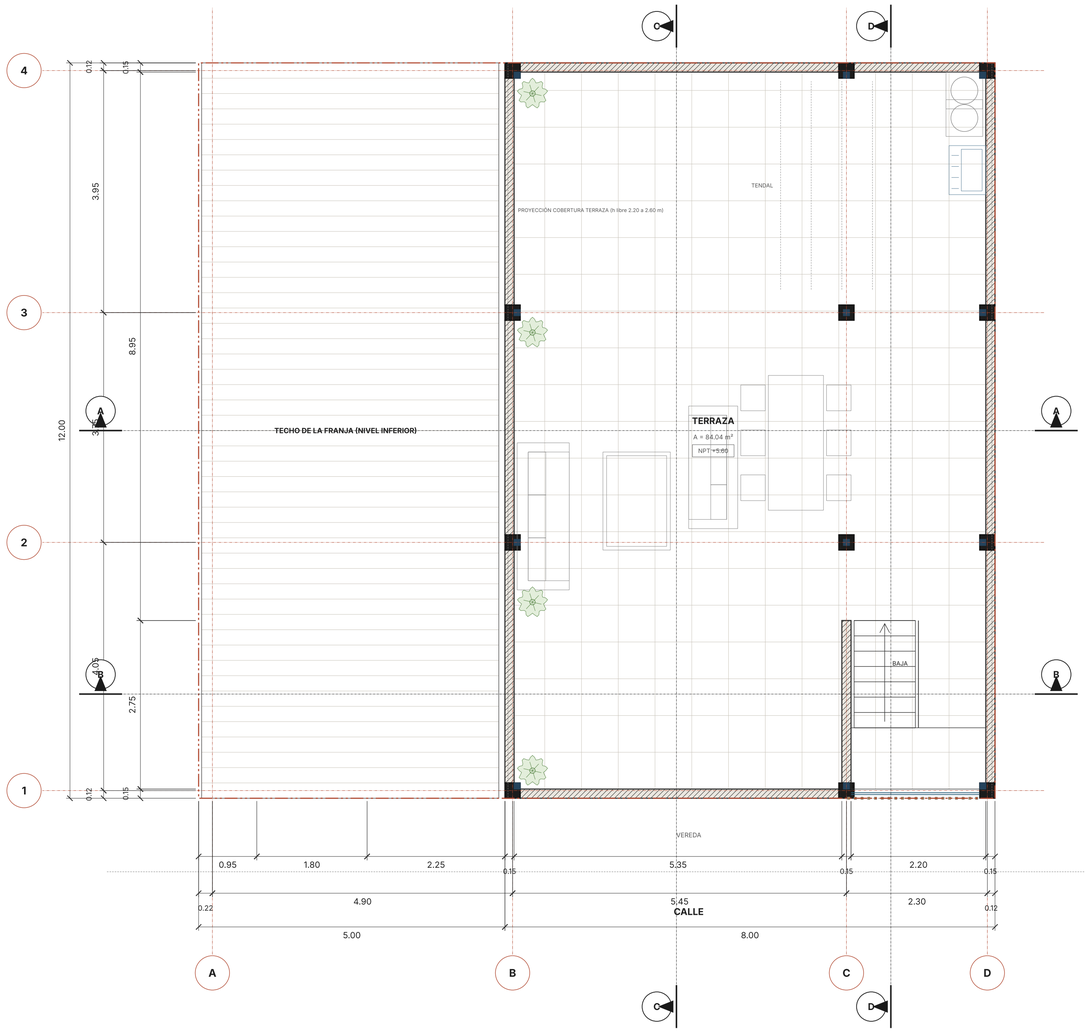

PLANTA TERRAZA (3er NIVEL)

ESC. 1/50 · NPT +5.60 | lavandería, tendal y sala exterior techada

LEYENDA

- Muro de albañilería (ladrillo KK 18 huecos)
- Columna / placa de concreto armado
- Proyección superior / elemento oculto
- Estructura metálica (tubo LAC ASTM A500)
- Eje estructural
- Vidrio / policarbonato

NOTAS GENERALES

1. Cotas y niveles en metros; verificar en obra antes de ejecutar.
2. Muros: albañilería confinada de ladrillo KK e=0.15; tabiques de baño e=0.10.
3. Losas aligeradas h=0.20; vigas 0.25×0.40; columnas 0.25×0.25.
4. Estructura referencial: diseño y firma de Ing. Civil colegiado (E.030, E.060, E.070, E.090).
5. Franja libre 5.00 × 12.00 SIN muros ni cerramientos: cochera para 2 autos y zona de reuniones.
6. Columnas metálicas de la franja sobre pedestales C°A° 0.40×0.40 (h=0.50 sobre piso) y zapatas.
7. Todos los dormitorios ventilan e iluminan hacia la franja techada (luz libre bajo cubierta 4.40 m).
8. Escalera: contrapaso 0.175, paso 0.25, ancho 1.00 m por tramo.

CASA LINTERNA

VIVIENDA UNIFAMILIAR · 2 PISOS + TERRAZA + FRANJA TECHADA

TERRENO
13.00 × 12.00 m = 156.00 m²

VIVIENDA
8.00 × 12.00 m · 2 pisos (material noble)

FRANJA LIBRE
5.00 × 12.00 m · cochera (cob. liviana)

PROPIETARIO
_____

UBICACIÓN
_____

PROYECTISTA
_____

CAP / CIP N°
_____

ESPECIALIDAD
ARQUITECTURA

ÍNDICE DE LÁMINAS


A-01 PLANTA 1er PISO
A-02 PLANTA 2do PISO
A-03 PLANTA DE TERRAZA
A-04 TECHOS, ESTRUCTURA METÁLICA Y DETALLES
A-05 CORTES TRANSVERSALES A-A Y B-B
A-06 CORTES LONGITUDINALES C-C Y D-D
A-07 ELEVACIONES
A-08 VISTAS 3D

LÁMINA
PLANTA DE TERRAZA

ESCALA
1/50


FECHA
OCTUBRE 2026

A-03

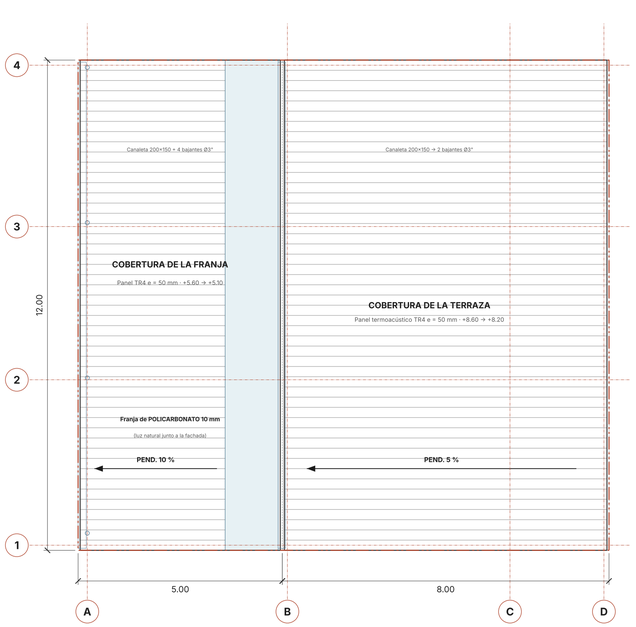

PLANTA DE TECHOS

ESC. 1/75 · coberturas a una sola agua

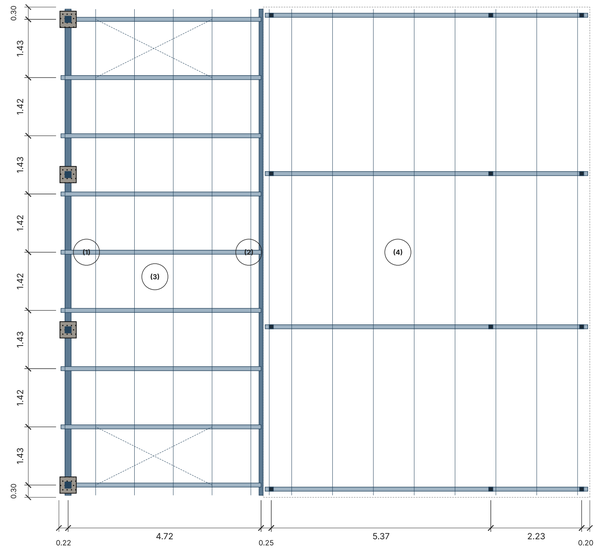

(1) VM-2 TUBO 150×300×4 sobre 4 columnas CM-1 150×150×4 con pedestales de C°A°


(2) AN-1 ÁNGULO L100×100×6 anclado a la viga de borde (lado vivienda)

(3) VM-1 TUBO 100×200×3 @1.425 · correas CO-1 50×100×2 @0.95 · arriostres Ø1/2"

(4) VT-1 TUBO 100×250×3 (4 ejes) · CT-1 TUBO 100×100×3 (12 und.) sobre columnas C°A° · CO-1 @1.00


ESTRUCTURA DE COBERTURAS

ESC. 1/75 · vigas, correas, columnas y arriostres

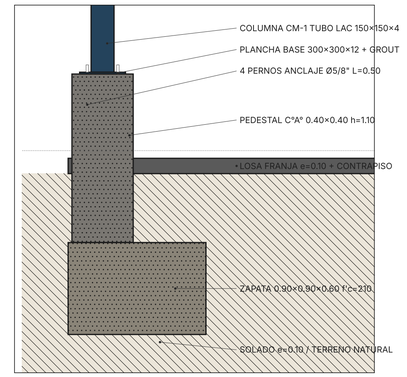

DETALLE 1 — PEDESTAL Y BASE

ESC. 1/20 · columna CM-1 de la franja

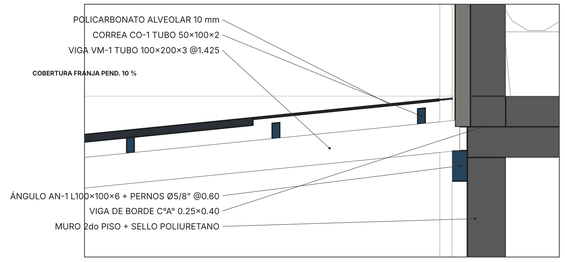

DETALLE 2 — APOYO EN LA VIVIENDA

ESC. 1/20 · ángulo AN-1 sobre viga de borde

CUADRO DE ELEMENTOS METÁLICOS — COBERTURA

CÓD.	ELEMENTO	SECCIÓN / ESPECIFICACIÓN	CANT.
CM-1	Columna franja	Tubo LAC 150×150×4 mm (h ≈ 4.0 m)	4
VM-2	Viga perimetral franja	Tubo LAC 150×300×4 mm	1
VM-1	Vigas de cubierta franja	Tubo LAC 100×200×3 mm @1.425	9
AN-1	Apoyo en vivienda	Ángulo L100×100×6 + pernos Ø5/8" @0.60	1
PD-1	Pedestal	C°A° 0.40×0.40 h=1.10, 4Ø5/8" + est. Ø3/8"	4
PL-1	Placa base	PL 300×300×12 + 4 pernos Ø5/8" L=0.50	4
CT-1	Columna terraza	Tubo LAC 100×100×3 mm + PL 200×200×9	12
VT-1	Viga terraza	Tubo LAC 100×250×3 mm	4
CO-1	Correas	Tubo LAC 50×100×2 mm @0.95-1.00	15
AR-1	Arriostres	Varilla lisa Ø1/2" con templador	8
CB-1	Cobertura	Panel termoacústico TR4 e=50 mm	~ 141 m²
CB-2	Franja de luz	Policarbonato alveolar 10 mm UV	~ 16 m²
CA-1	Canaletas + bajantes	Plancha galv. e=0.9 mm + 6 Ø3" PVC	2

CASA LINTERNA

VIVIENDA UNIFAMILIAR · 2 PISOS + TERRAZA + FRANJA TECHADA

TERRENO
13.00 × 12.00 m = 156.00 m²

VIVIENDA
8.00 × 12.00 m · 2 pisos (material noble)

FRANJA LIBRE
5.00 × 12.00 m · cochera (cob. liviana)

PROPIETARIO
_____

UBICACIÓN
_____

PROYECTISTA
_____

CAP / CIP N°
_____

ESPECIALIDAD
ARQUITECTURA

ÍNDICE DE LÁMINAS


A-01 PLANTA 1er PISO
A-02 PLANTA 2do PISO
A-03 PLANTA DE TERRAZA
A-04 TECHOS, ESTRUCTURA METÁLICA Y DETALLES
A-05 CORTES TRANSVERSALES A-A Y B-B
A-06 CORTES LONGITUDINALES C-C Y D-D
A-07 ELEVACIONES
A-08 VISTAS 3D

LÁMINA
TECHOS, ESTRUCTURA METÁLICA Y DETALLES

ESCALA
INDICADA


FECHA
OCTUBRE 2026

A-04

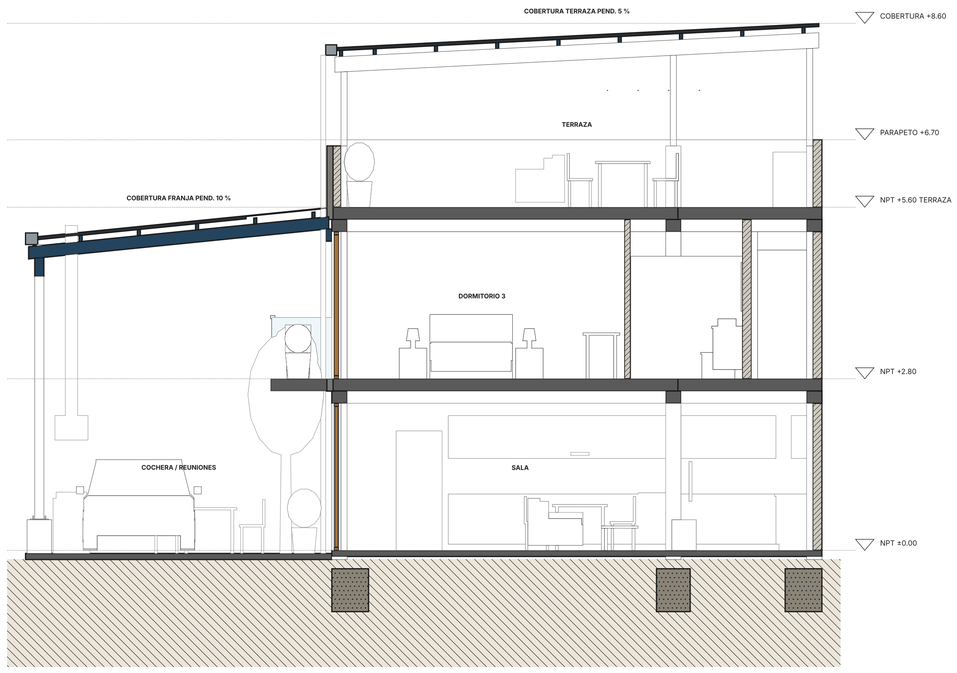

CORTE A-A

ESC. 1/50 · por dormitorios 3 y sala, mirando al fondo

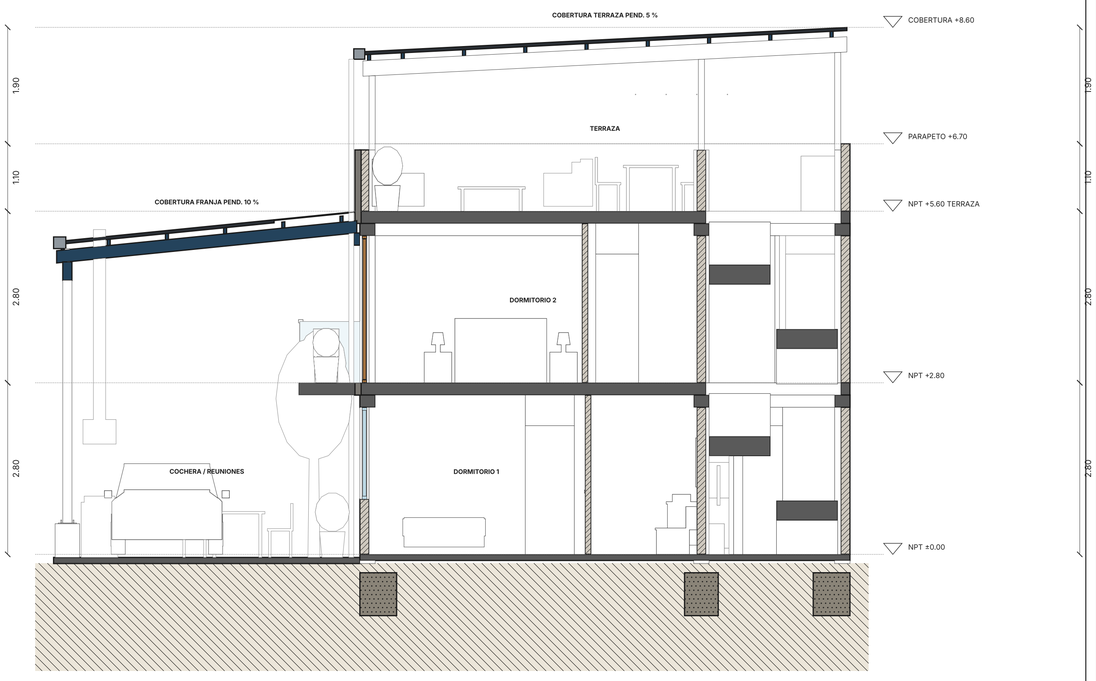

CORTE B-B

ESC. 1/50 · por escalera y dormitorios 1 y 2

CASA LINTERNA

VIVIENDA UNIFAMILIAR · 2 PISOS + TERRAZA + FRANJA TECHADA

TERRENO
13.00 × 12.00 m = 156.00 m²

VIVIENDA
8.00 × 12.00 m · 2 pisos (material noble)

FRANJA LIBRE
5.00 × 12.00 m · cochera (cob. liviana)

PROPIETARIO
_____

UBICACIÓN
_____

PROYECTISTA
_____

CAP / CIP N°
_____

ESPECIALIDAD
ARQUITECTURA

ÍNDICE DE LÁMINAS

A-01 PLANTA 1er PISO
A-02 PLANTA 2do PISO
A-03 PLANTA DE TERRAZA
A-04 TECHOS, ESTRUCTURA METÁLICA Y DETALLES
A-05 CORTES TRANSVERSALES A-A Y B-B
A-06 CORTES LONGITUDINALES C-C Y D-D
A-07 ELEVACIONES
A-08 VISTAS 3D

LÁMINA
CORTES TRANSVERSALES A-A Y B-B

ESCALA
1/50


FECHA
OCTUBRE 2026

A-05



CORTE C-C

ESC. 1/50 · por dormitorios, mirando a la franja

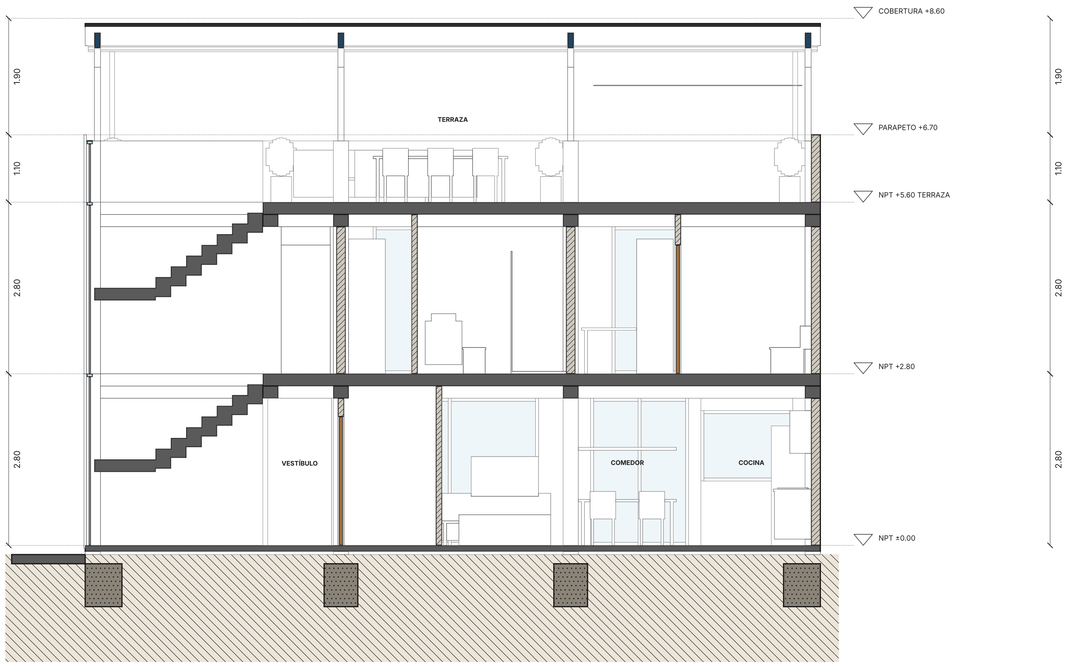

CORTE D-D

ESC. 1/50 · por escalera, pasillo y baños

CASA LINTERNA

VIVIENDA UNIFAMILIAR · 2 PISOS + TERRAZA + FRANJA TECHADA

TERRENO
13.00 × 12.00 m = 156.00 m²

VIVIENDA
8.00 × 12.00 m · 2 pisos (material noble)

FRANJA LIBRE
5.00 × 12.00 m · cochera (cob. liviana)

PROPIETARIO
_____

UBICACIÓN
_____

PROYECTISTA
_____

CAP / CIP N°
_____

ESPECIALIDAD
ARQUITECTURA

ÍNDICE DE LÁMINAS


A-01 PLANTA 1er PISO
A-02 PLANTA 2do PISO
A-03 PLANTA DE TERRAZA
A-04 TECHOS, ESTRUCTURA METÁLICA Y DETALLES
A-05 CORTES TRANSVERSALES A-A Y B-B
A-06 CORTES LONGITUDINALES C-C Y D-D
A-07 ELEVACIONES
A-08 VISTAS 3D

LÁMINA
CORTES LONGITUDINALES C-C Y D-D

ESCALA
1/50

FECHA
OCTUBRE 2026

A-06

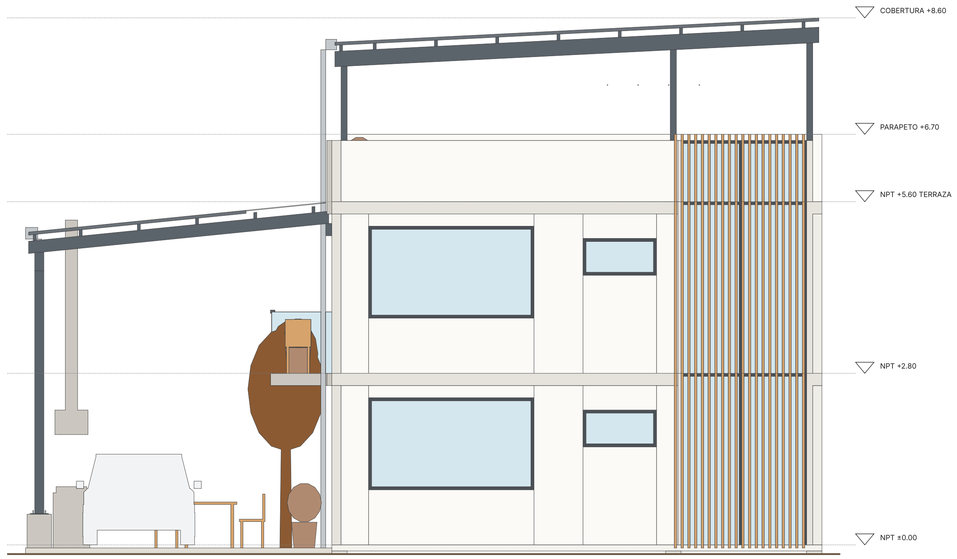

ELEVACIÓN PRINCIPAL (CALLE)

ESC. 1/50 · franja abierta + linterna de celosía




ELEVACIÓN HACIA LA FRANJA

ESC. 1/50 · ventanas y balcones de todos los ambientes



VISTA DESDE LA CALLE

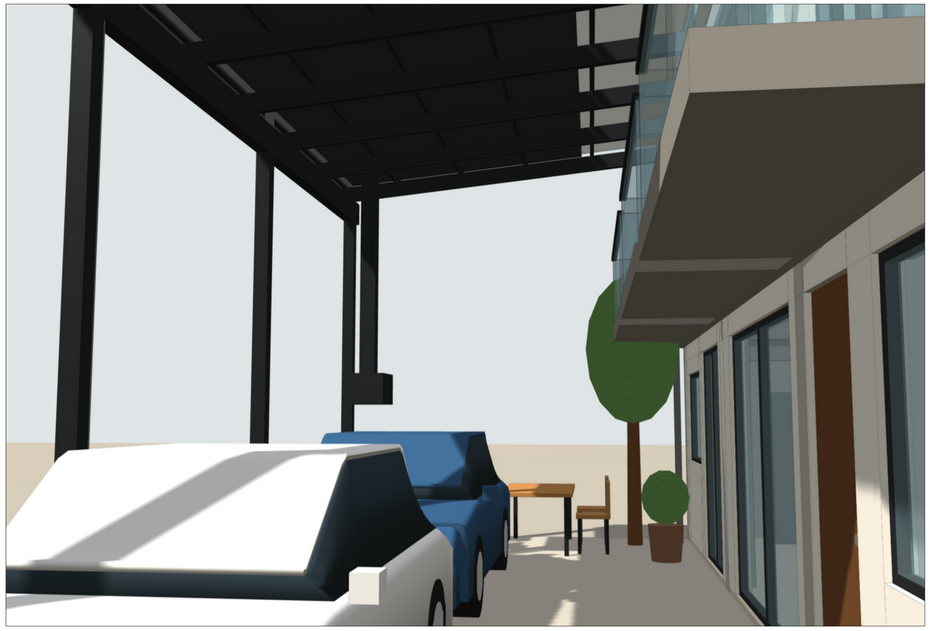

FRANJA TECHADA: COCHERA Y REUNIONES

CASA LINTERNA

VIVIENDA UNIFAMILIAR · 2 PISOS + TERRAZA + FRANJA TECHADA

TERRENO
13.00 × 12.00 m = 156.00 m²

VIVIENDA
8.00 × 12.00 m · 2 pisos (material noble)

FRANJA LIBRE
5.00 × 12.00 m · cochera (cob. liviana)

PROPIETARIO
_____

UBICACIÓN
_____

PROYECTISTA
_____

CAP / CIP N°
_____

ESPECIALIDAD
ARQUITECTURA

ÍNDICE DE LÁMINAS

A-01 PLANTA 1er PISO
A-02 PLANTA 2do PISO
A-03 PLANTA DE TERRAZA
A-04 TECHOS, ESTRUCTURA METÁLICA Y DETALLES
A-05 CORTES TRANSVERSALES A-A Y B-B
A-06 CORTES LONGITUDINALES C-C Y D-D
A-07 ELEVACIONES
A-08 VISTAS 3D

LÁMINA
ELEVACIONES

ESCALA
1/50

FECHA
OCTUBRE 2026

A-07




ISOMÉTRICA GENERAL



CORTE FUGADO LONGITUDINAL



2do PISO — 3 DORMITORIOS CON BAÑO Y BALCÓN

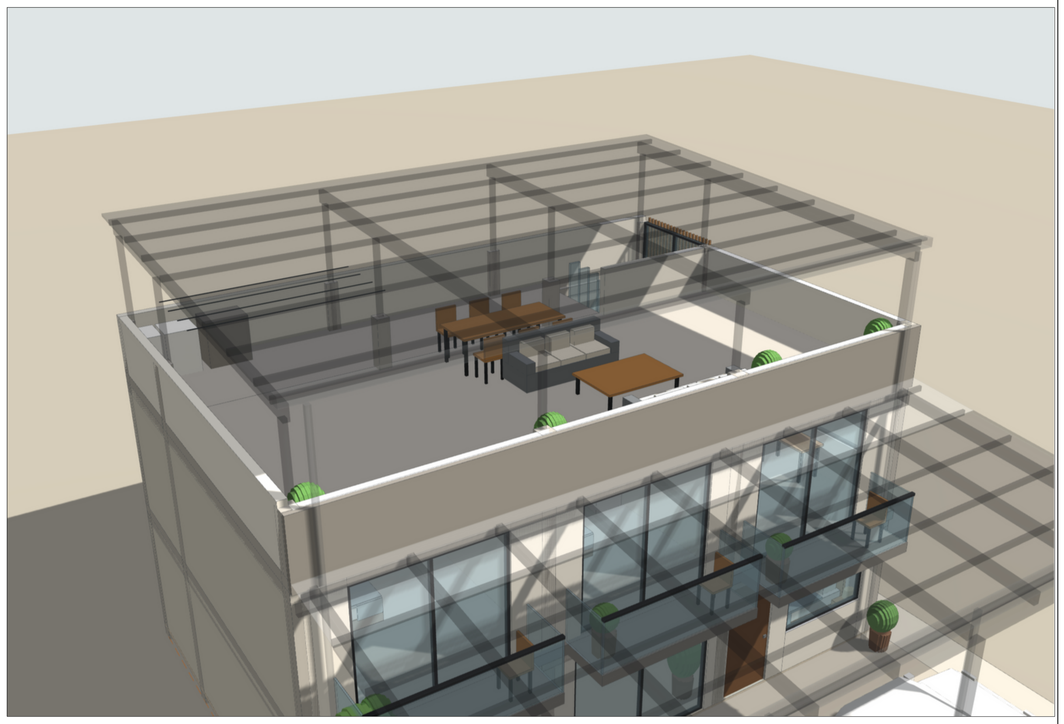

TERRAZA (COBERTURA EN TRANSPARENCIA)

CASA LINTERNA

VIVIENDA UNIFAMILIAR · 2 PISOS + TERRAZA + FRANJA TECHADA

TERRENO
13.00 × 12.00 m = 156.00 m²

VIVIENDA
8.00 × 12.00 m · 2 pisos (material noble)

FRANJA LIBRE
5.00 × 12.00 m · cochera (cob. liviana)

PROPIETARIO
_____

UBICACIÓN
_____

PROYECTISTA
_____

CAP / CIP N°
_____

ESPECIALIDAD
ARQUITECTURA

ÍNDICE DE LÁMINAS

A-01 PLANTA 1er PISO
A-02 PLANTA 2do PISO
A-03 PLANTA DE TERRAZA
A-04 TECHOS, ESTRUCTURA METÁLICA Y DETALLES
A-05 CORTES TRANSVERSALES A-A Y B-B
A-06 CORTES LONGITUDINALES C-C Y D-D
A-07 ELEVACIONES
A-08 VISTAS 3D

LÁMINA
VISTAS 3D

ESCALA
S/E

FECHA
OCTUBRE 2026

A-08