
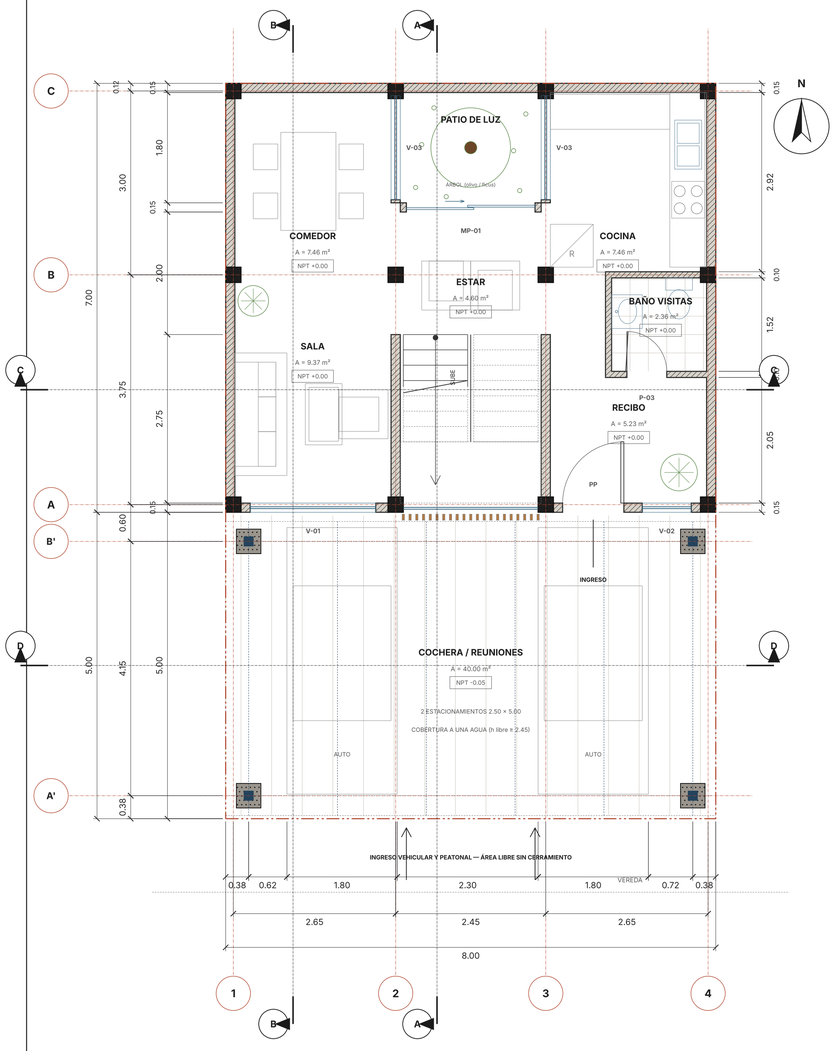


PLANTA 1er PISO — GENERAL

ESC. 1/50 · NPT ±0.00 | sala, comedor, cocina + cochera libre

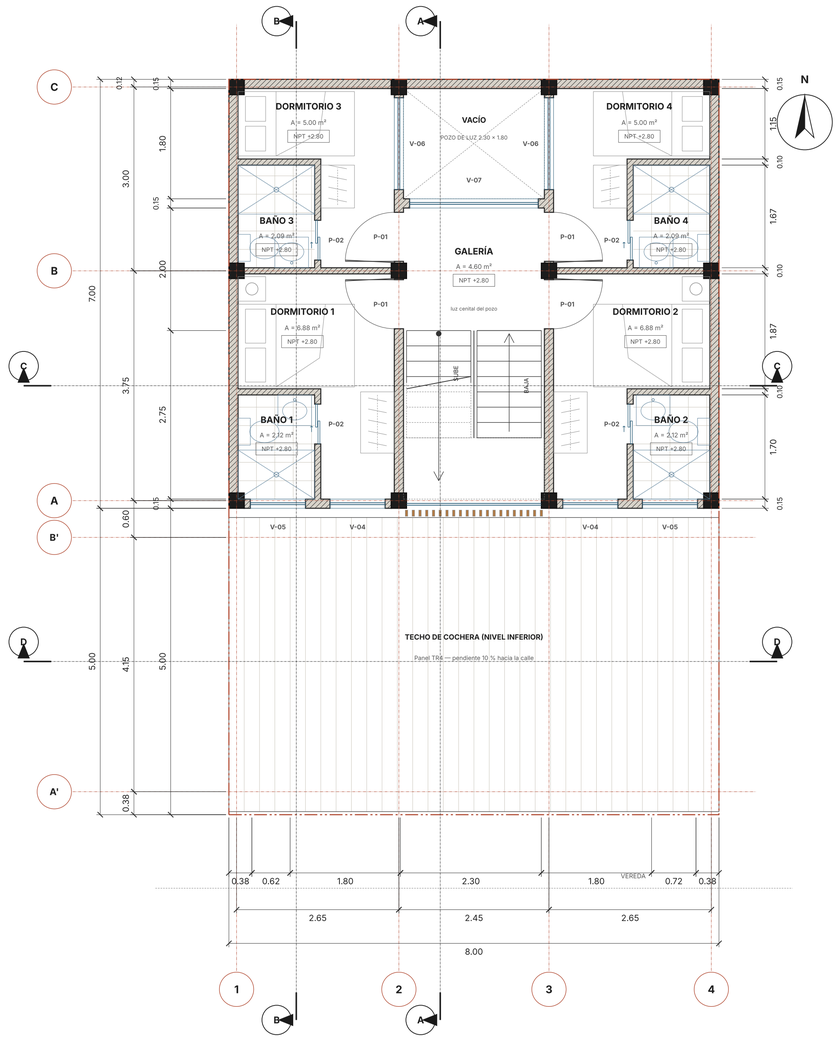

PLANTA 2do PISO

ESC. 1/50 · NPT +2.80 | 4 dormitorios con baño propio

CUADRO DE VANOS

CÓD.	TIPO	ANCHO	ALTO	ALF.	CANT.	DESCRIPCIÓN
P-01	PUERTA	0.80	2.10	0.00	4	Dormitorio frontal
P-02	PUERTA	0.65	2.10	0.00	4	Puerta corrediza baño
P-03	PUERTA	0.65	2.10	0.00	1	Baño de visitas
PP	PUERTA	1.00	2.40	0.00	1	Puerta principal pivotante de madera
MP-01	PUERTA	2.10	2.40	0.00	1	Mampara corrediza estar-patio de luz
V-01	VENTANA	2.05	2.10	0.30	1	Ventanal sala hacia la cochera
V-02	VENTANA	0.80	1.50	0.90	1	Ventana recibo
V-03	VENTANA	1.70	2.40	0.00	2	Paño fijo de vidrio comedor-patio
V-04	VENTANA	0.90	1.50	0.90	2	Ventana dormitorio
V-05	VENTANA	0.90	0.60	1.60	2	Ventana alta baño
V-06	VENTANA	1.50	1.20	1.00	2	Ventana dormitorio al pozo de luz
V-07	VENTANA	2.10	1.50	0.90	1	Paño fijo galería-pozo de luz

CUADRO DE AMBIENTES

NIV.	AMBIENTE	m²	ACABADO DE PISO
1°	COCHERA / REUNIONES	40.00	Concreto estampado
1°	SALA	9.37	Porcelanato 60×120
1°	RECIBO	5.23	Porcelanato 60×120
1°	BAÑO VISITAS	2.36	Cerámico antideslizante
1°	ESTAR	4.60	Porcelanato 60×120
1°	COMEDOR	7.46	Porcelanato 60×120
1°	COCINA	7.46	Porcelanato 60×120
1°	PATIO DE LUZ	4.14	Canto rodado + jardín
2°	DORMITORIO 1	6.88	Piso laminado
2°	BAÑO 1	2.12	Porcelanato
2°	DORMITORIO 2	6.88	Piso laminado
2°	BAÑO 2	2.12	Porcelanato
2°	DORMITORIO 3	5.00	Piso laminado
2°	BAÑO 3	2.09	Porcelanato
2°	DORMITORIO 4	5.00	Piso laminado
2°	BAÑO 4	2.09	Porcelanato
2°	GALERÍA	4.60	Piso laminado
3°	TERRAZA	41.12	Porcelanato antideslizante
3°	LAVANDERÍA	3.44	Cerámico antideslizante

CASA LINTERNA

VIVIENDA UNIFAMILIAR · 2 PISOS + TERRAZA + COCHERA

TERRENO
8.00 × 12.00 m = 96.00 m²

VIVIENDA
8.00 × 7.00 m · 2 pisos (material noble)

ÁREA LIBRE
8.00 × 5.00 m · cochera (cob. liviana)

PROPIETARIO
_____

UBICACIÓN
_____

PROYECTISTA
_____

CAP / CIP N°
_____

ESPECIALIDAD
ARQUITECTURA

ÍNDICE DE LÁMINAS


A-01 PLANTAS 1er Y 2do PISO
A-02 PLANTA DE TERRAZA Y TECHOS
A-03 CORTES LONGITUDINALES A-A Y B-B
A-04 CORTES, ESTRUCTURA METÁLICA Y DETALLES
A-05 ELEVACIONES
A-06 VISTAS 3D

LÁMINA
PLANTAS 1er Y 2do PISO

ESCALA
1/50


FECHA
OCTUBRE 2026

A-01

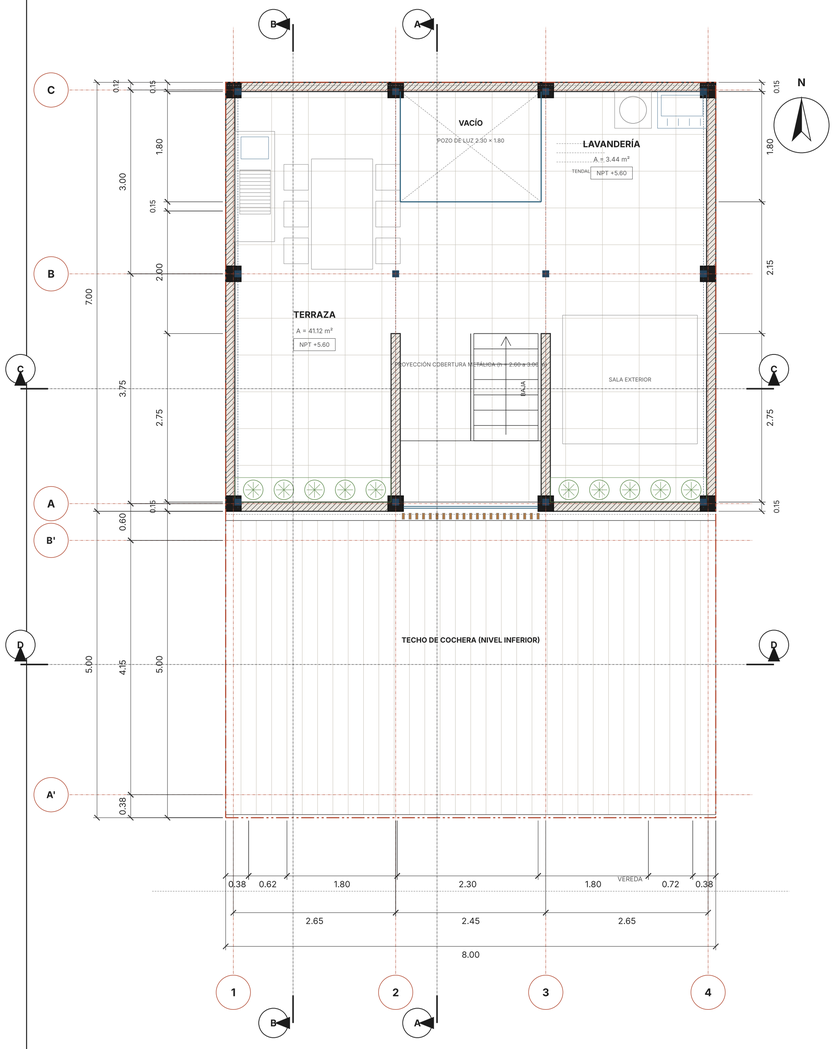

PLANTA TERRAZA (3er NIVEL)

ESC. 1/50 · NPT +5.60 | lavandería, parrilla y sala exterior

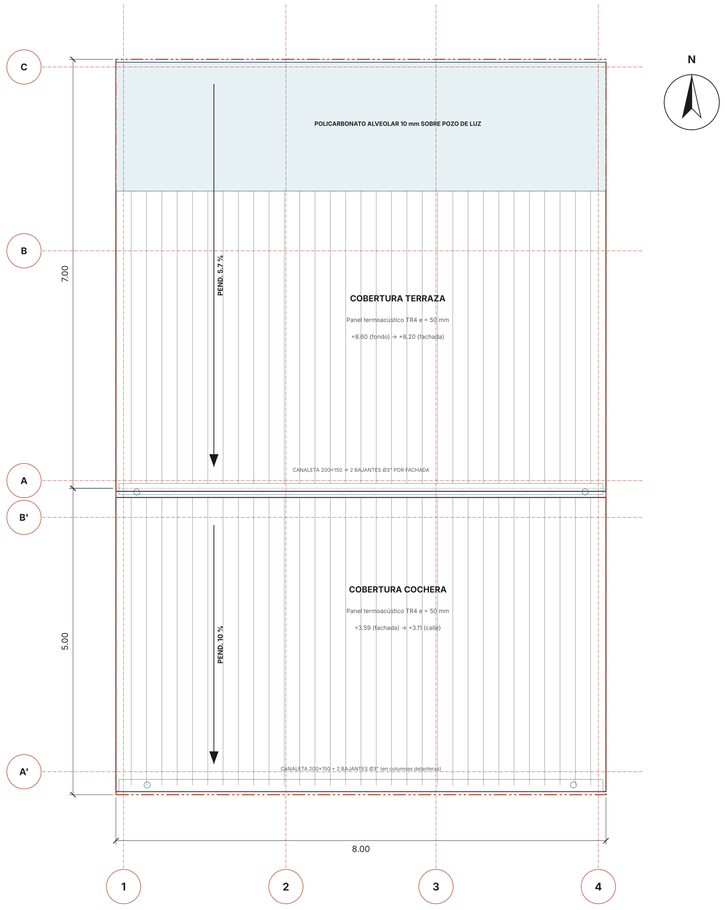

PLANTA DE TECHOS

ESC. 1/50 · coberturas metálicas a una sola agua

CUADRO DE ÁREAS

ÍTEM	MEDIDAS (m)	ÁREA (m²)
TERRENO	8.00 × 12.00	96.00
ÁREA TECHADA 1er PISO	8.00 × 7.00	56.00
ÁREA TECHADA 2do PISO	8.00 × 7.00	56.00
TOTAL MATERIAL NOBLE		**112.00**
TERRAZA (cobertura liviana)	8.00 × 7.00	56.00
ÁREA LIBRE — COCHERA (cob. liviana)	8.00 × 5.00	40.00 (41.7 %)
POZO DE LUZ (desde 1er piso)	2.30 × 1.80	4.14

LEYENDA

- Muro de albañilería (ladrillo KK 18 huecos)
- Columna / placa de concreto armado
- Proyección superior / elemento oculto
- Estructura metálica (tubo LAC ASTM A500)
- Eje estructural
- Vidrio / policarbonato

NOTAS GENERALES

1. Cotas y niveles en metros; verificar en obra antes de ejecutar.
2. Muros: albañilería confinada de ladrillo KK e=0.15; tabiques de baño e=0.10; tarrajeo frotachado.
3. Losas aligeradas h=0.20 m; vigas 0.25×0.40 m; columnas C-1 0.25×0.25 m.
4. Estructura referencial: requiere diseño por Ing. Civil colegiado (E.020, E.030, E.060, E.070, E.090).
5. Cochera: área libre SIN muros ni cerramientos; cobertura desmontable a una sola agua; h libre mín. 2.45 m.
6. Columnas metálicas sobre pedestales de C*A* 0.40×0.40 (h=0.50 sobre piso) y zapatas 0.90×0.90.
7. Dormitorios posteriores ventilan e iluminan por pozo de luz 2.30 m (perpendicular al vano).
8. Baños 3 y 4 ventilan por ducto/extractor a la terraza. Escalera: cp 0.175, paso 0.25, ancho 1.05 m.

CASA LINTERNA

VIVIENDA UNIFAMILIAR · 2 PISOS + TERRAZA + COCHERA

TERRENO
8.00 × 12.00 m = 96.00 m²

VIVIENDA
8.00 × 7.00 m · 2 pisos (material noble)

ÁREA LIBRE
8.00 × 5.00 m · cochera (cob. liviana)

PROPIETARIO
_____

UBICACIÓN
_____

PROYECTISTA
_____

CAP / CIP N°
_____

ESPECIALIDAD
ARQUITECTURA

ÍNDICE DE LÁMINAS


A-01 PLANTAS 1er Y 2do PISO
A-02 PLANTA DE TERRAZA Y TECHOS
A-03 CORTES LONGITUDINALES A-A Y B-B
A-04 CORTES, ESTRUCTURA METÁLICA Y DETALLES
A-05 ELEVACIONES
A-06 VISTAS 3D

LÁMINA
PLANTA DE TERRAZA Y TECHOS

ESCALA
1/50

FECHA
OCTUBRE 2026

A-02

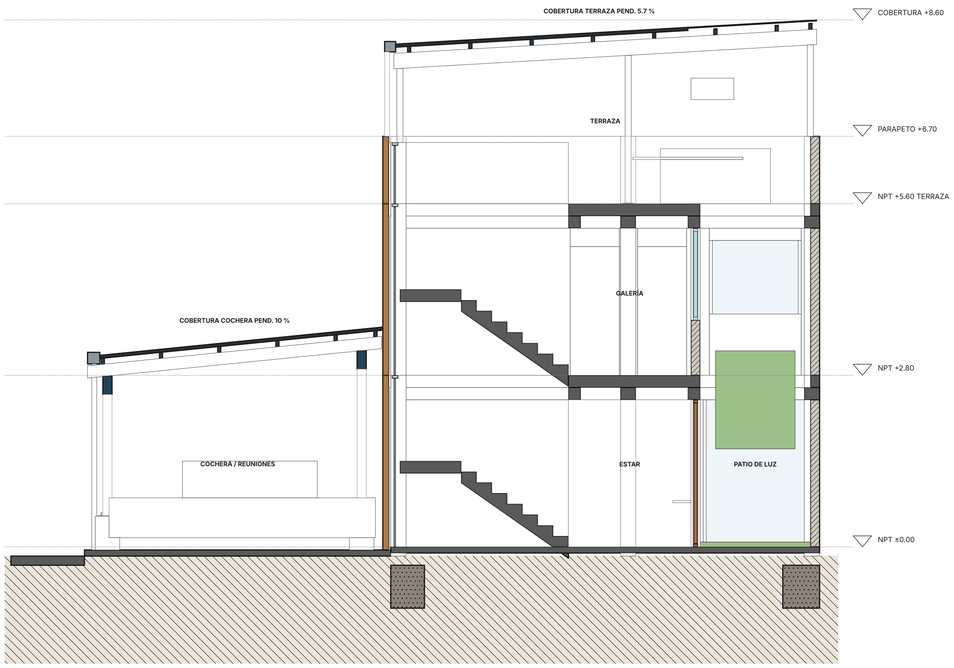

CORTE A-A

ESC. 1/50 · por escalera, galería y pozo de luz



CORTE B-B

ESC. 1/50 · por dormitorios, cochera y terraza

CASA LINTERNA

VIVIENDA UNIFAMILIAR · 2 PISOS + TERRAZA + COCHERA

TERRENO
8.00 × 12.00 m = 96.00 m²

VIVIENDA
8.00 × 7.00 m · 2 pisos (material noble)

ÁREA LIBRE
8.00 × 5.00 m · cochera (cob. liviana)

PROPIETARIO
_____

UBICACIÓN
_____

PROYECTISTA
_____

CAP / CIP N°
_____

ESPECIALIDAD
ARQUITECTURA

ÍNDICE DE LÁMINAS


A-01 PLANTAS 1er Y 2do PISO
A-02 PLANTA DE TERRAZA Y TECHOS
A-03 CORTES LONGITUDINALES A-A Y B-B
A-04 CORTES, ESTRUCTURA METÁLICA Y DETALLES
A-05 ELEVACIONES
A-06 VISTAS 3D

LÁMINA
CORTES LONGITUDINALES A-A Y B-B

ESCALA
1/50

FECHA
OCTUBRE 2026

A-03

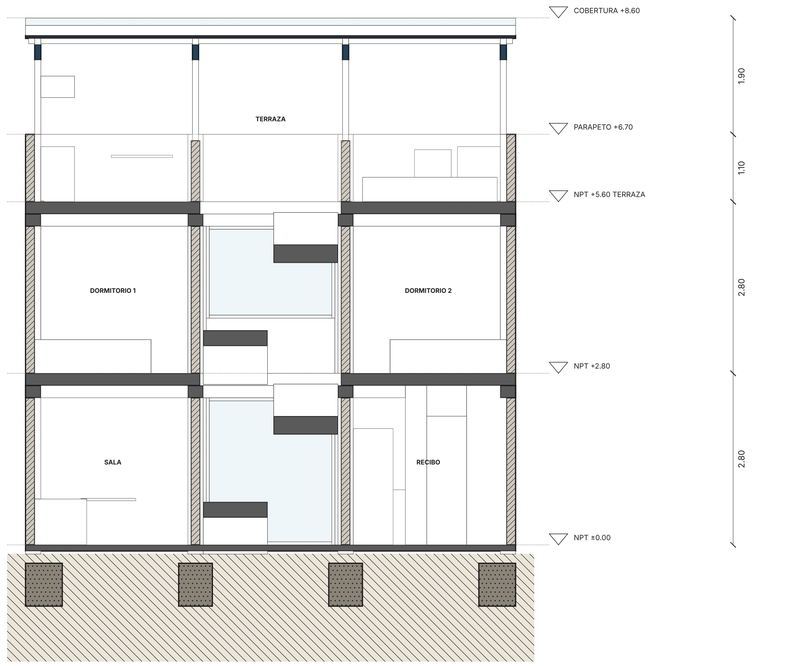


CORTE C-C

ESC. 1/50 · por escalera y dormitorios frontales



CORTE D-D

ESC. 1/50 · por la cochera, mirando a la fachada

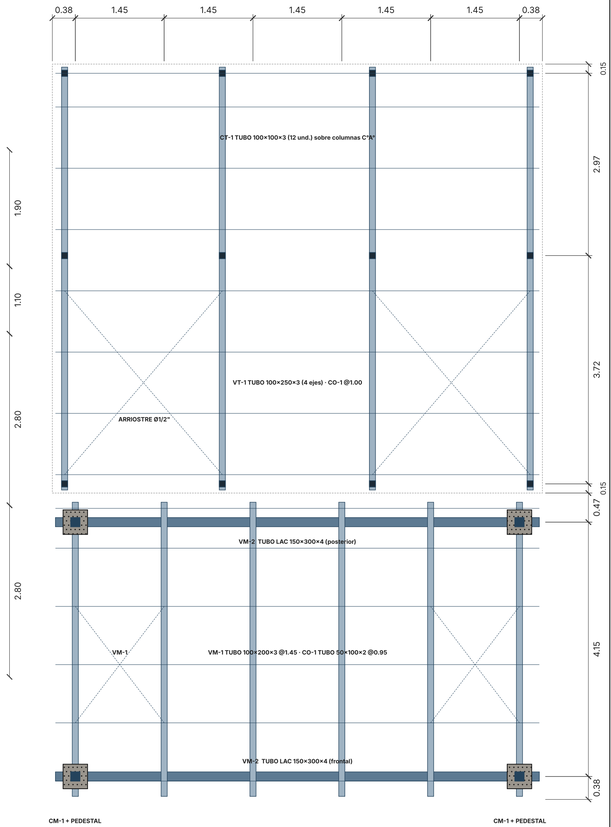


ESTRUCTURA DE COBERTURAS

ESC. 1/50 · planta — vigas, correas, columnas y arriostres


CUADRO DE ELEMENTOS METÁLICOS — COBERTURA

CÓD.	ELEMENTO	SECCIÓN / ESPECIFICACIÓN	CANT.
CM-1	Columna cochera	Tubo LAC 150×150×4 mm	4
VM-2	Viga principal cochera	Tubo LAC 150×300×4 mm	2
VM-1	Viga secundaria cochera	Tubo LAC 100×200×3 mm @1.45	6
PD-1	Pedestal	C°A° 0.40×0.40 h=1.10, 4Ø5/8" + est. Ø3/8"	4
PL-1	Placa base	PL 300×300×12 + 4 pernos Ø5/8" L=0.50	4
CT-1	Columna terraza	Tubo LAC 100×100×3 mm + PL 200×200×9	12
VT-1	Viga terraza	Tubo LAC 100×250×3 mm	4
CO-1	Correas	Tubo LAC 50×100×2 mm @0.95-1.00	14
AR-1	Arriostres	Varilla lisa Ø1/2" con templador	8
CB-1	Cobertura	Panel termoacústico TR4 e=50 mm	~ 79 m²
CB-2	Franja de luz	Policarbonato alveolar 10 mm UV	~ 17 m²
CA-1	Canaletas + bajantes	Plancha galv. e=0.9 mm + 4 Ø3" PVC	2
—	Acabado	Anticorrosivo epóxico + esmalte poliuretano grafito	

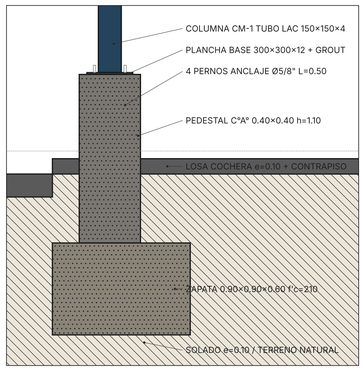

DETALLE 1 — PEDESTAL Y BASE

ESC. 1/20 · columna CM-1 de cochera

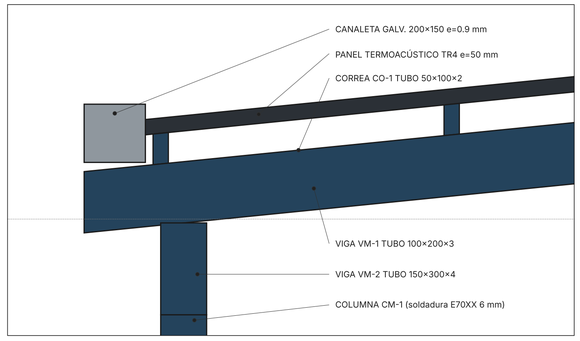

DETALLE 2 — APOYO DE COBERTURA

ESC. 1/10 · VM-2 / VM-1 sobre CM-1

CASA LINTERNA

VIVIENDA UNIFAMILIAR · 2 PISOS + TERRAZA + COCHERA

TERRENO
8.00 × 12.00 m = 96.00 m²

VIVIENDA
8.00 × 7.00 m · 2 pisos (material noble)

ÁREA LIBRE
8.00 × 5.00 m · cochera (cob. liviana)

PROPIETARIO
_____

UBICACIÓN
_____

PROYECTISTA
_____

CAP / CIP N°
_____

ESPECIALIDAD
ARQUITECTURA

ÍNDICE DE LÁMINAS


A-01 PLANTAS 1er Y 2do PISO
A-02 PLANTA DE TERRAZA Y TECHOS
A-03 CORTES LONGITUDINALES A-A Y B-B
A-04 CORTES, ESTRUCTURA METÁLICA Y DETALLES
A-05 ELEVACIONES
A-06 VISTAS 3D

LÁMINA
CORTES, ESTRUCTURA METÁLICA Y DETALLES

ESCALA
INDICADA


FECHA
OCTUBRE 2026

A-04

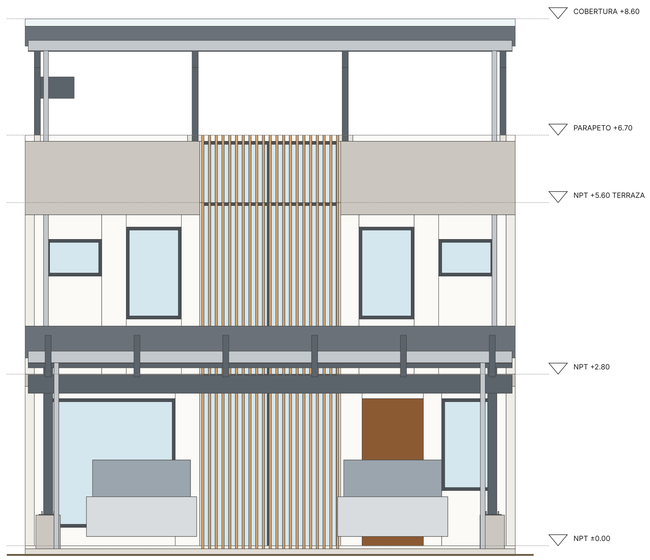


ELEVACIÓN PRINCIPAL (CALLE)

ESC. 1/50 · cochera abierta + linterna de celosía

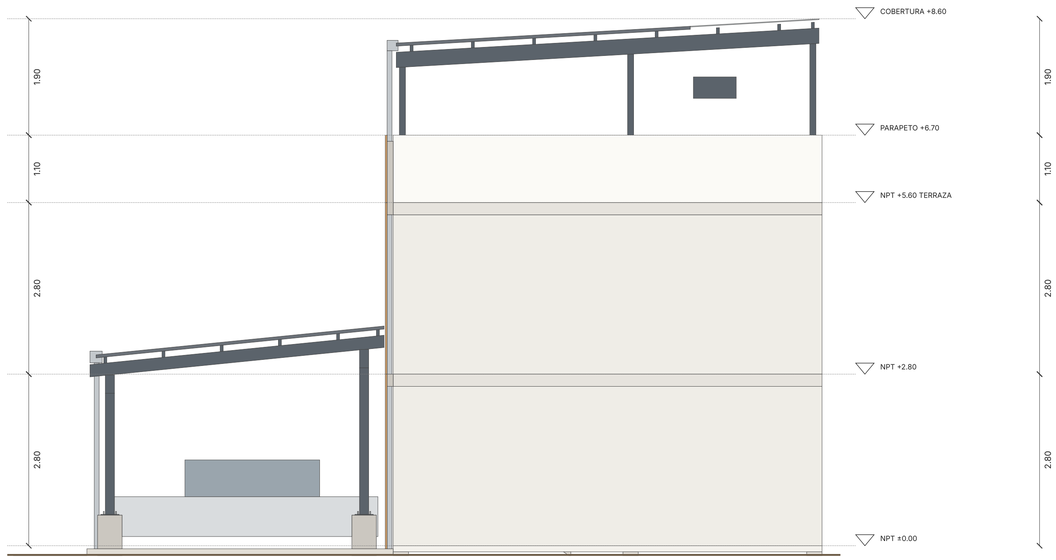

ELEVACIÓN LATERAL

ESC. 1/50 · perfil de las coberturas a una sola agua

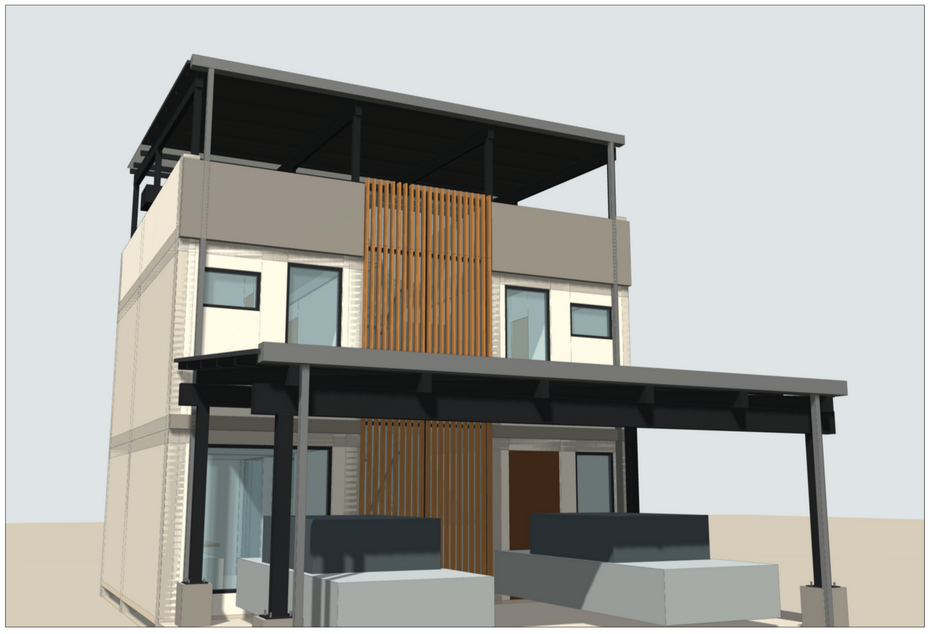

VISTA DESDE LA CALLE



COCHERA / ÁREA DE REUNIONES

CASA LINTERNA

VIVIENDA UNIFAMILIAR · 2 PISOS + TERRAZA + COCHERA

TERRENO
8.00 × 12.00 m = 96.00 m²

VIVIENDA
8.00 × 7.00 m · 2 pisos (material noble)

ÁREA LIBRE
8.00 × 5.00 m · cochera (cob. liviana)

PROPIETARIO
_____

UBICACIÓN
_____

PROYECTISTA
_____

CAP / CIP N°
_____

ESPECIALIDAD
ARQUITECTURA

ÍNDICE DE LÁMINAS


A-01 PLANTAS 1er Y 2do PISO
A-02 PLANTA DE TERRAZA Y TECHOS
A-03 CORTES LONGITUDINALES A-A Y B-B
A-04 CORTES, ESTRUCTURA METÁLICA Y DETALLES
A-05 ELEVACIONES
A-06 VISTAS 3D

LÁMINA
ELEVACIONES


ESCALA
1/50

FECHA
OCTUBRE 2026


A-05

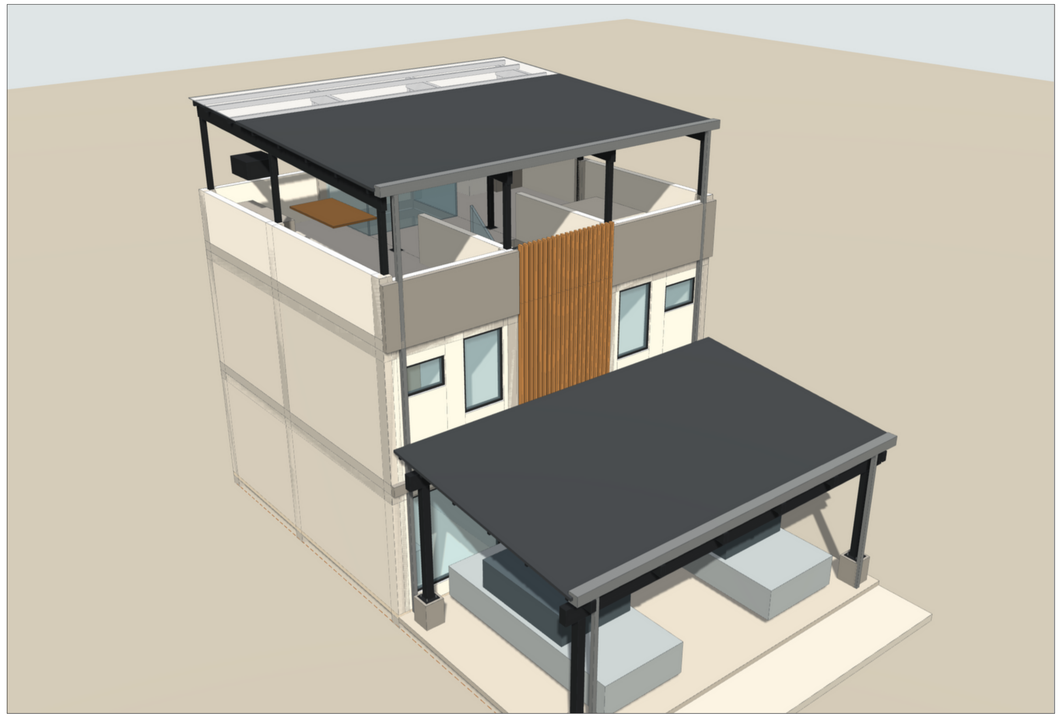


ISOMÉTRICA GENERAL

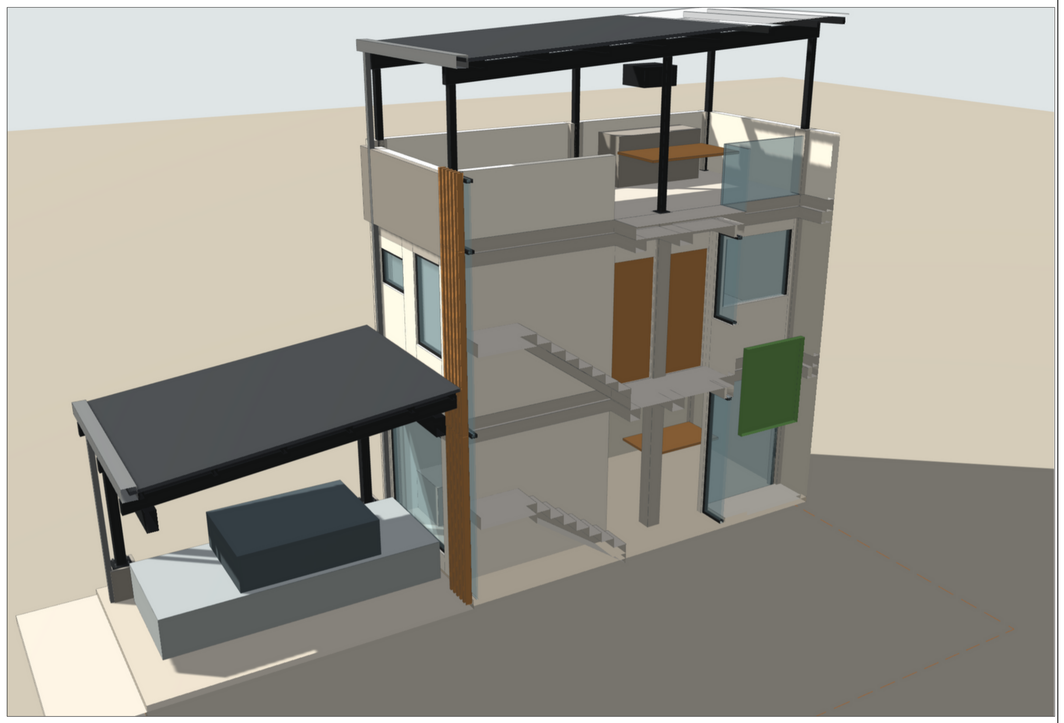

CORTE FUGADO LONGITUDINAL

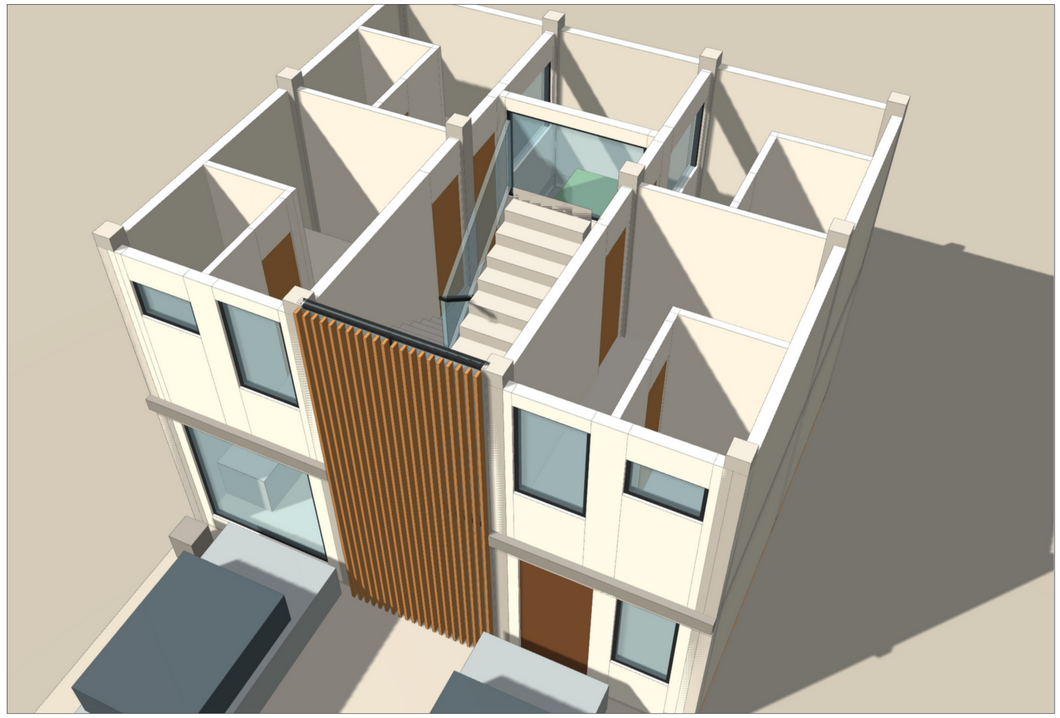

2do PISO — 4 DORMITORIOS CON BAÑO

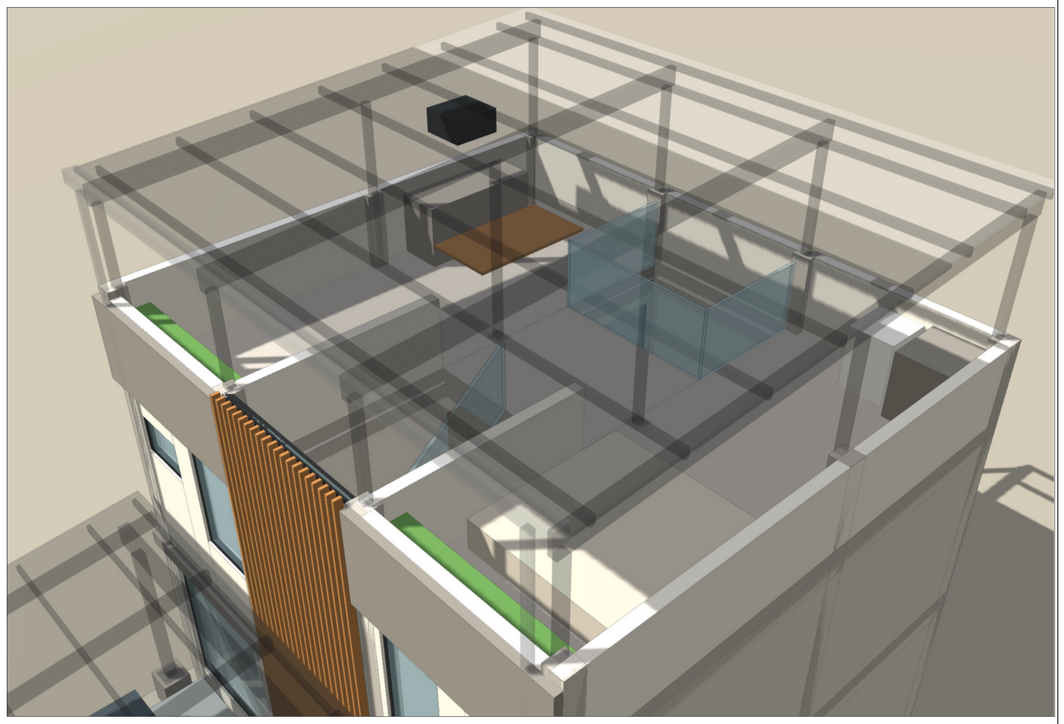

TERRAZA (COBERTURA EN TRANSPARENCIA)

CASA LINTERNA

VIVIENDA UNIFAMILIAR · 2 PISOS + TERRAZA + COCHERA

TERRENO
8.00 × 12.00 m = 96.00 m²

VIVIENDA
8.00 × 7.00 m · 2 pisos (material noble)

ÁREA LIBRE
8.00 × 5.00 m · cochera (cob. liviana)

PROPIETARIO
_____

UBICACIÓN
_____

PROYECTISTA
_____

CAP / CIP N°
_____

ESPECIALIDAD
ARQUITECTURA

ÍNDICE DE LÁMINAS

A-01 PLANTAS 1er Y 2do PISO
A-02 PLANTA DE TERRAZA Y TECHOS
A-03 CORTES LONGITUDINALES A-A Y B-B
A-04 CORTES, ESTRUCTURA METÁLICA Y DETALLES
A-05 ELEVACIONES
A-06 VISTAS 3D

LÁMINA
VISTAS 3D

ESCALA
S/E

FECHA
OCTUBRE 2026

A-06