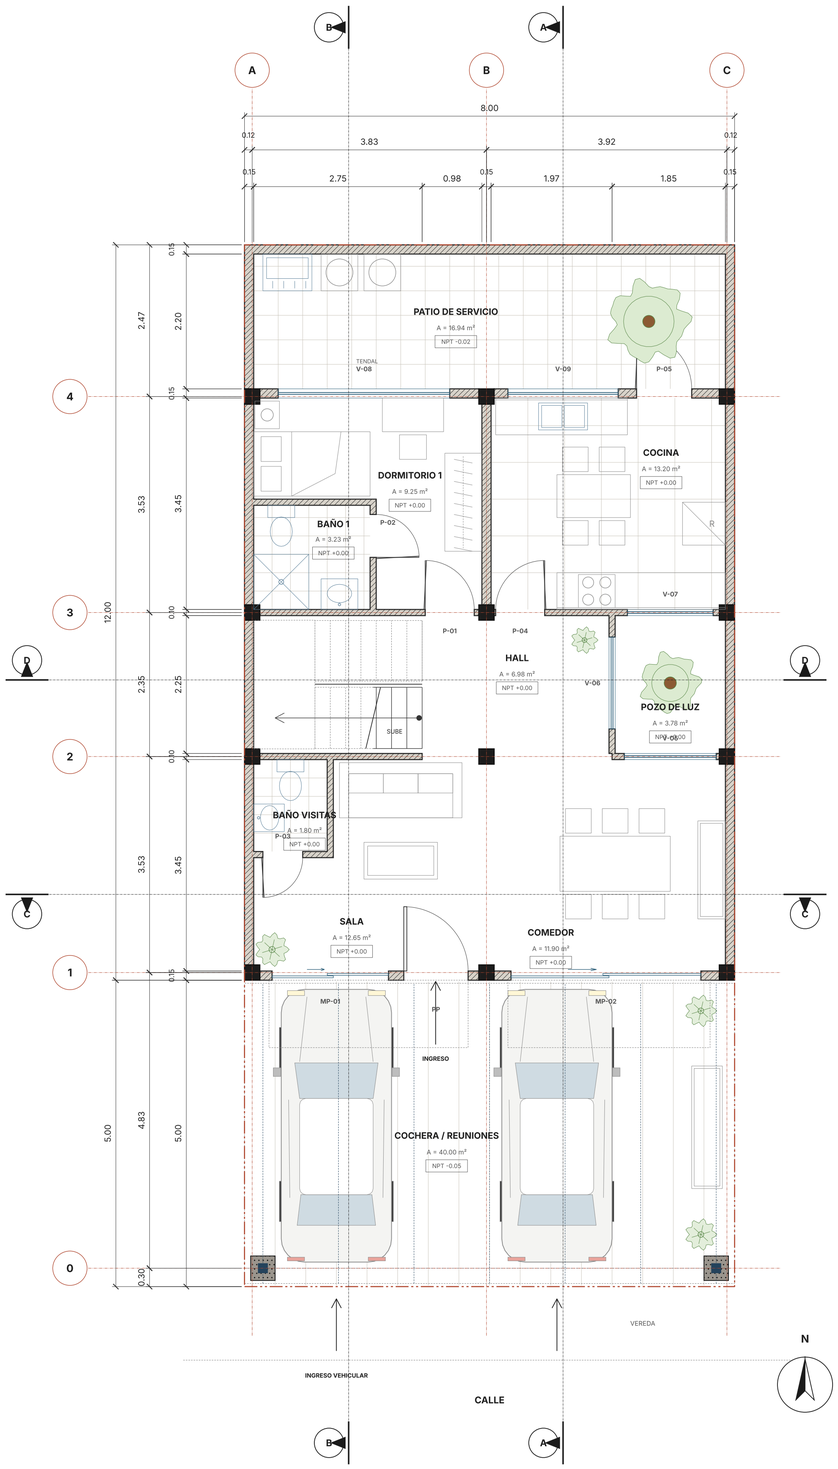


PLANTA 1er PISO — GENERAL

ESC. 1/50 · NPT ±0.00 | cochera, sala, comedor, cocina, dormitorio con baño

CUADRO DE VANOS

CÓD.	TIPO	ANCHO	ALTO	ALF.	CANT.	DESCRIPCIÓN
P-01	PUERTA	0.80	2.10	0.00	5	Puerta de dormitorio
P-02	PUERTA	0.70	2.10	0.00	5	Baño de dormitorio
P-03	PUERTA	0.65	2.10	0.00	1	Baño de visitas
P-04	PUERTA	0.80	2.10	0.00	1	Puerta de cocina
P-05	PUERTA	0.90	2.10	0.00	1	Puerta cocina-patio de servicio
PP	PUERTA	1.05	2.40	0.00	1	Puerta principal pivotante de madera
MP-01	PUERTA	1.90	2.40	0.00	1	Mampara corrediza sala-cochera
MP-02	PUERTA	3.10	2.40	0.00	1	Mampara corrediza comedor-cochera
MP-03	PUERTA	2.50	2.40	0.00	2	Mampara corrediza a balcón
V-05	VENTANA	1.50	2.10	0.30	1	Paño fijo comedor-pozo de luz
V-06	VENTANA	1.50	1.30	0.90	2	Ventana hall-pozo de luz
V-07	VENTANA	1.40	1.15	1.05	1	Ventana cocina-pozo de luz
V-08	VENTANA	2.80	1.50	0.90	1	Ventana dormitorio al patio
V-09	VENTANA	1.80	1.15	1.05	1	Ventana cocina al patio
V-10	VENTANA	1.40	0.60	1.60	2	Ventana alta baño-pozo de luz
V-11	VENTANA	2.80	1.50	0.90	2	Ventana dormitorio al patio

CASA LINTERNA

VIVIENDA UNIFAMILIAR · 2 PISOS + TERRAZA + COCHERA TECHADA

TERRENO
8.00 × 17.00 m = 136.00 m²

VIVIENDA
8.00 × 12.00 m · 2 pisos (material noble)

COCHERA
8.00 × 5.00 m · al frente (cob. liviana)

PROPIETARIO
_____

UBICACIÓN
_____

PROYECTISTA
_____

CAP / CIP N°
_____

ESPECIALIDAD
ARQUITECTURA

ÍNDICE DE LÁMINAS


A-01 PLANTA 1er PISO
A-02 PLANTA 2do PISO
A-03 PLANTA DE TERRAZA
A-04 TECHOS, ESTRUCTURA METÁLICA Y DETALLES
A-05 CORTES LONGITUDINALES A-A Y B-B
A-06 CORTES TRANSVERSALES Y ELEVACIONES
A-07 VISTAS EXTERIORES
A-08 VISTAS 3D

LÁMINA
PLANTA 1er PISO

ESCALA
1/50

FECHA
OCTUBRE 2026

A-01

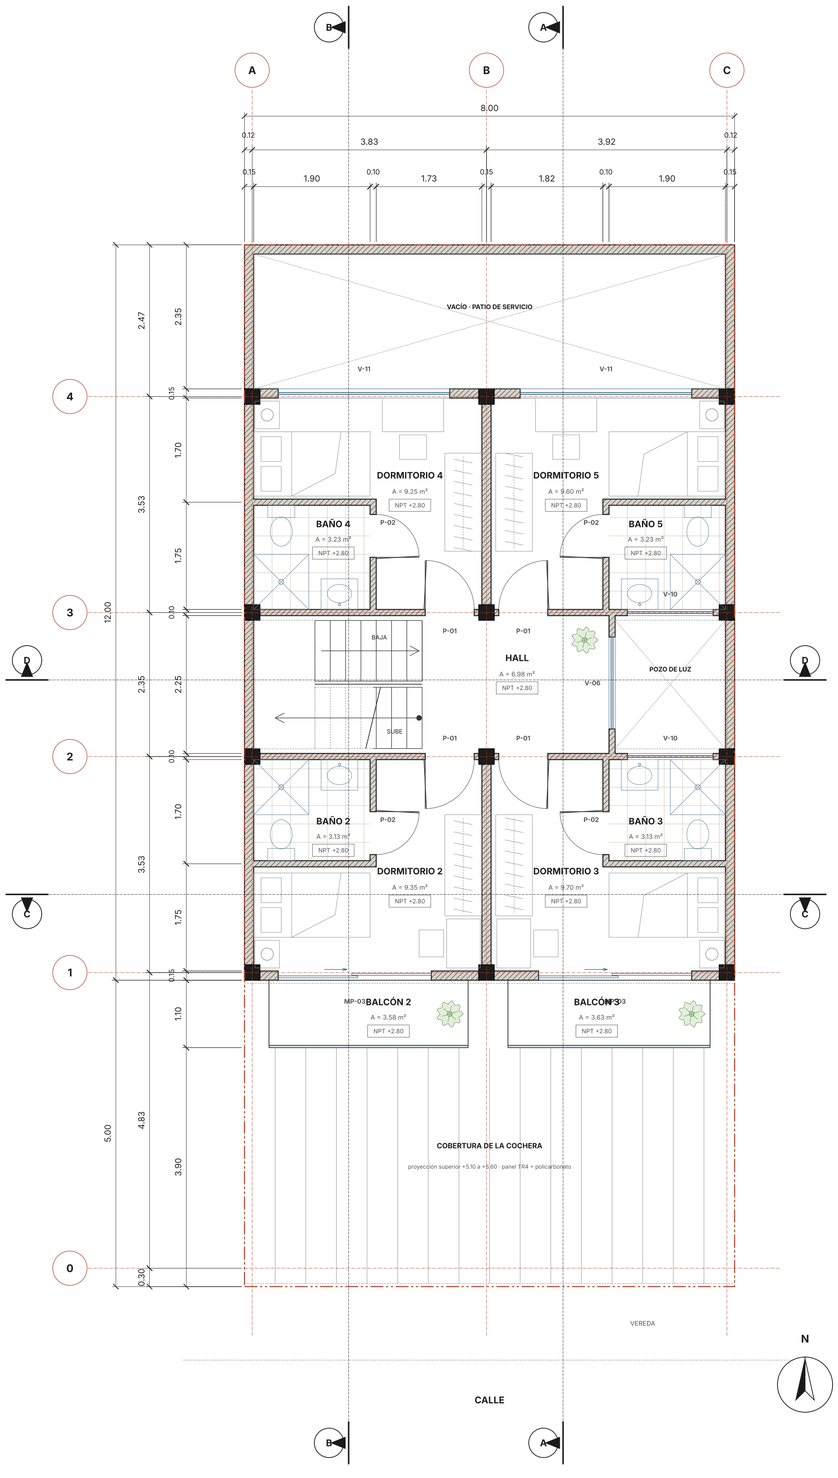

PLANTA 2do PISO

ESC. 1/50 · NPT +2.80 | 4 dormitorios con baño, 2 con balcón a la cochera

CUADRO DE AMBIENTES

NIV.	AMBIENTE	m²	ACABADO DE PISO
1°	COCHERA / REUNIONES	40.00	Concreto estampado
1°	SALA	12.65	Porcelanato 60×120
1°	COMEDOR	11.90	Porcelanato 60×120
1°	BAÑO VISITAS	1.80	Cerámico
1°	HALL	6.98	Porcelanato 60×120
1°	POZO DE LUZ	3.78	Canto rodado
1°	DORMITORIO 1	9.25	Piso laminado
1°	BAÑO 1	3.23	Porcelanato
1°	COCINA	13.20	Porcelanato 60×120
1°	PATIO DE SERVICIO	16.94	Cerámico antideslizante
2°	DORMITORIO 2	9.35	Piso laminado
2°	BAÑO 2	3.13	Porcelanato
2°	DORMITORIO 3	9.70	Piso laminado
2°	BAÑO 3	3.13	Porcelanato
2°	BALCÓN 2	3.58	Porcelanato antideslizante
2°	BALCÓN 3	3.63	Porcelanato antideslizante
2°	HALL	6.98	Piso laminado
2°	DORMITORIO 4	9.25	Piso laminado
2°	BAÑO 4	3.23	Porcelanato
2°	DORMITORIO 5	9.60	Piso laminado
2°	BAÑO 5	3.23	Porcelanato
3°	TERRAZA	62.44	Porcelanato antideslizante

CUADRO DE ÁREAS

ÍTEM	MEDIDAS (m)	ÁREA (m²)
TERRENO	8.00 × 17.00	136.00
ÁREA TECHADA 1er PISO	8.00 × 9.65 - pozo de luz	73.42
ÁREA TECHADA 2do PISO	8.00 × 9.65 - pozo de luz	73.42
BALCONES (volados sobre la cochera)	2 × 3.30 × 1.10	7.21
TOTAL MATERIAL NOBLE		**154.05**
TERRAZA (cobertura liviana)	8.00 × 9.65	77.20
COCHERA / REUNIONES (cob. liviana)	8.00 × 5.00	40.00 (29.4 %)
PATIO DE SERVICIO + POZO DE LUZ (abiertos)	8.00 × 2.35 + 1.80 × 2.10	22.58 (16.6 %)

CASA LINTERNA

VIVIENDA UNIFAMILIAR · 2 PISOS + TERRAZA + COCHERA TECHADA

TERRENO
8.00 × 17.00 m = 136.00 m²

VIVIENDA
8.00 × 12.00 m · 2 pisos (material noble)

COCHERA
8.00 × 5.00 m · al frente (cob. liviana)

PROPIETARIO
_____

UBICACIÓN
_____

PROYECTISTA
_____

CAP / CIP N°
_____

ESPECIALIDAD
ARQUITECTURA

ÍNDICE DE LÁMINAS


A-01 PLANTA 1er PISO
A-02 PLANTA 2do PISO
A-03 PLANTA DE TERRAZA
A-04 TECHOS, ESTRUCTURA METÁLICA Y DETALLES
A-05 CORTES LONGITUDINALES A-A Y B-B
A-06 CORTES TRANSVERSALES Y ELEVACIONES
A-07 VISTAS EXTERIORES
A-08 VISTAS 3D

LÁMINA
PLANTA 2do PISO

ESCALA
1/50

FECHA
OCTUBRE 2026

A-02

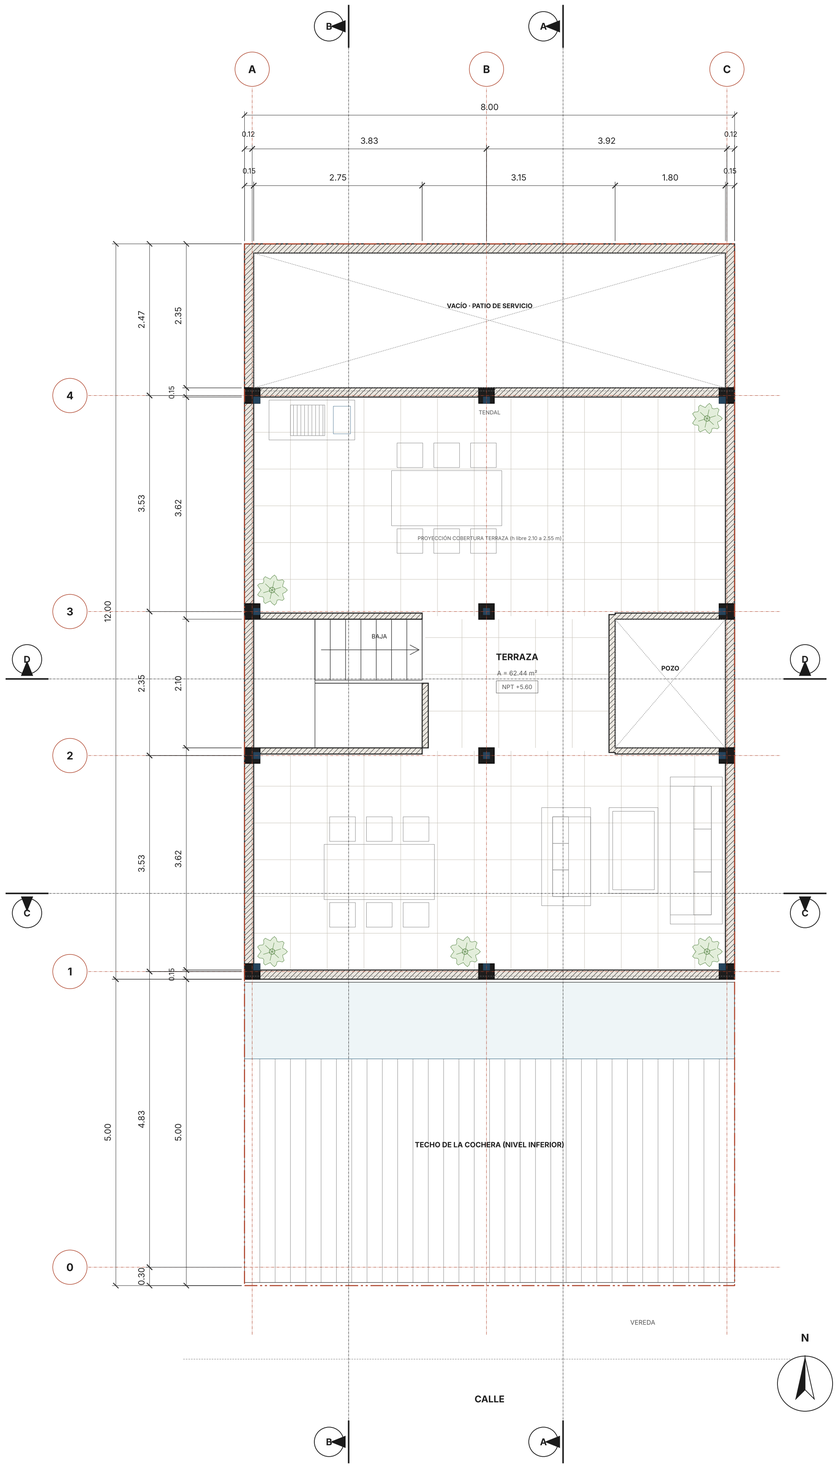

PLANTA TERRAZA (3er NIVEL)

ESC. 1/50 · NPT +5.60 | terraza techada con parrilla, sala y comedor exterior

LEYENDA

- Muro de albañilería (ladrillo KK 18 huecos)
- Columna / placa de concreto armado
- Proyección superior / elemento oculto
- Estructura metálica (tubo LAC ASTM A500)
- Eje estructural
- Vidrio / policarbonato

NOTAS GENERALES

1. Cotas y niveles en metros; verificar en obra antes de ejecutar.
2. Muros: albañilería confinada de ladrillo KK e=0.15; tabiques de baño e=0.10.
3. Losas aligeradas h=0.20; vigas 0.25×0.40; columnas 0.25×0.25.
4. Estructura referencial: diseño y firma de Ing. Civil colegiado (E.030, E.060, E.070, E.090).
5. Cochera 8.00 × 5.00 SIN muros ni cerramientos: 2 autos lado a lado o zona de reuniones.
6. Columnas metálicas de la cochera sobre pedestales C*A* 0.40×0.40 (h=0.50 sobre piso) y zapatas.
7. Sala, comedor y dormitorios 2 y 3 (con balcón) miran a la cochera; dorm. 1, 4, 5 y cocina al patio.
8. Baños 3 y 5, hall y cocina ventilan al pozo de luz; baños 1, 2 y 4 por ducto (extractor).
9. Escalera: contrapaso 0.175, paso 0.25, ancho 1.00 m por tramo.

CASA LINTERNA

VIVIENDA UNIFAMILIAR · 2 PISOS + TERRAZA + COCHERA TECHADA

TERRENO
8.00 × 17.00 m = 136.00 m²

VIVIENDA
8.00 × 12.00 m · 2 pisos (material noble)

COCHERA
8.00 × 5.00 m · al frente (cob. liviana)

PROPIETARIO
_____

UBICACIÓN
_____

PROYECTISTA
_____

CAP / CIP N°
_____

ESPECIALIDAD
ARQUITECTURA

ÍNDICE DE LÁMINAS


A-01 PLANTA 1er PISO
A-02 PLANTA 2do PISO
A-03 PLANTA DE TERRAZA
A-04 TECHOS, ESTRUCTURA METÁLICA Y DETALLES
A-05 CORTES LONGITUDINALES A-A Y B-B
A-06 CORTES TRANSVERSALES Y ELEVACIONES
A-07 VISTAS EXTERIORES
A-08 VISTAS 3D

LÁMINA
PLANTA DE TERRAZA

ESCALA
1/50


FECHA
OCTUBRE 2026

A-03

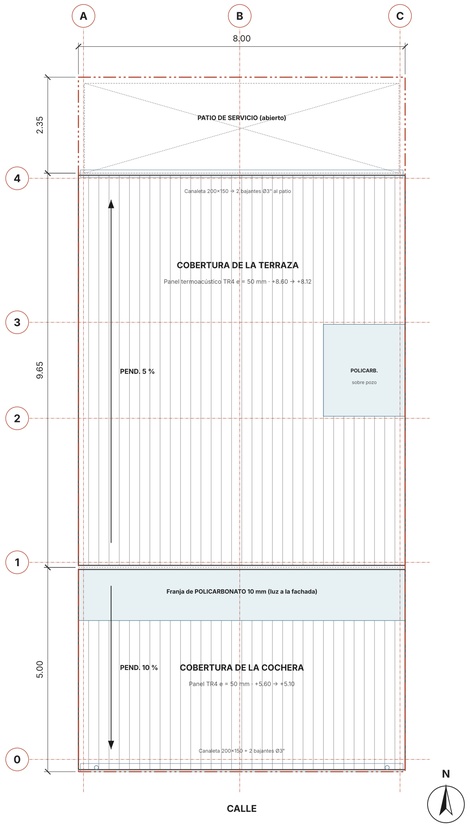

PLANTA DE TECHOS

ESC. 1/75 · coberturas a una sola agua

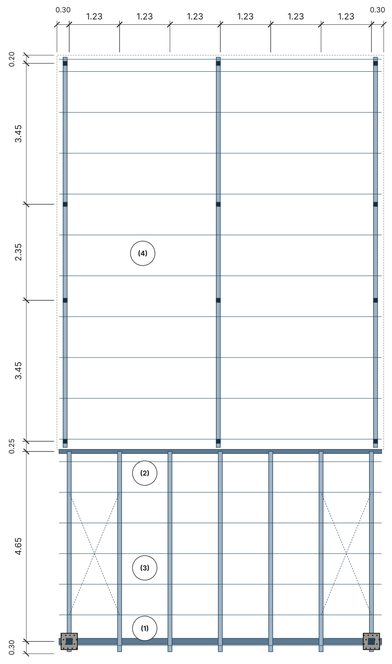

(1) VM-2 TUBO 150×300×4 sobre 2 columnas CM-1 150×150×4 con pedestales de C°A°


(2) AN-1 ÁNGULO L100×100×6 anclado a la viga de borde (lado vivienda)

(3) VM-1 TUBO 100×200×3 @1.233 · correas CO-1 50×100×2 @0.75 · arriostres Ø1/2"

(4) VT-1 TUBO 100×250×3 (3 ejes) · CT-1 TUBO 100×100×3 (12 und.) sobre columnas C°A° · CO-1 @1.00


ESTRUCTURA DE COBERTURAS

ESC. 1/75 · vigas, correas, columnas y arriostres

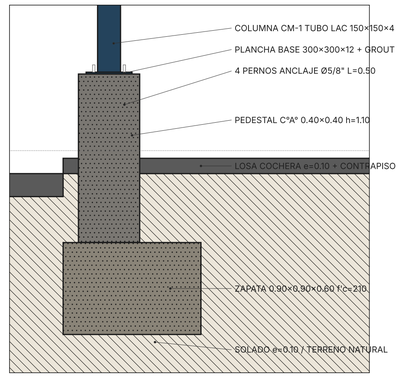

DETALLE 1 — PEDESTAL Y BASE

ESC. 1/20 · columna CM-1 de la cochera

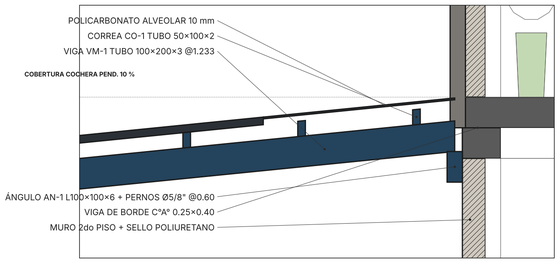

DETALLE 2 — APOYO EN LA VIVIENDA

ESC. 1/20 · ángulo AN-1 sobre viga de borde

CUADRO DE ELEMENTOS METÁLICOS — COBERTURA

CÓD.	ELEMENTO	SECCIÓN / ESPECIFICACIÓN	CANT.
CM-1	Columna cochera	Tubo LAC 150×150×4 mm (h = 4.0 m)	2
VM-2	Viga frontal cochera	Tubo LAC 150×300×4 mm (L = 7.90 m)	1
VM-1	Vigas de cubierta cochera	Tubo LAC 100×200×3 mm @1.233	7
AN-1	Apoyo en vivienda	Ángulo L100×100×6 + pernos Ø5/8" @0.60	1
PD-1	Pedestal	C°A° 0.40×0.40 h=1.10, 4Ø5/8" + est. Ø3/8"	2
PL-1	Placa base	PL 300×300×12 + 4 pernos Ø5/8" L=0.50	2
CT-1	Columna terraza	Tubo LAC 100×100×3 mm + PL 200×200×9	12
VT-1	Viga terraza	Tubo LAC 100×250×3 mm	3
CO-1	Correas	Tubo LAC 50×100×2 mm @0.75-1.00	18
AR-1	Arriostres	Varilla lisa Ø1/2" con templador	4
CB-1	Cobertura	Panel termoacústico TR4 e=50 mm	~ 101 m²
CB-2	Paños de luz	Policarbonato alveolar 10 mm UV	~ 15 m²
CA-1	Canaletas + bajantes	Plancha galv. e=0.9 mm + 4 Ø3" PVC	2

CASA LINTERNA

VIVIENDA UNIFAMILIAR · 2 PISOS + TERRAZA + COCHERA TECHADA

TERRENO
8.00 × 17.00 m = 136.00 m²

VIVIENDA
8.00 × 12.00 m · 2 pisos (material noble)

COCHERA
8.00 × 5.00 m · al frente (cob. liviana)

PROPIETARIO
_____

UBICACIÓN
_____

PROYECTISTA
_____

CAP / CIP N°
_____

ESPECIALIDAD
ARQUITECTURA

ÍNDICE DE LÁMINAS


A-01 PLANTA 1er PISO
A-02 PLANTA 2do PISO
A-03 PLANTA DE TERRAZA
A-04 TECHOS, ESTRUCTURA METÁLICA Y DETALLES
A-05 CORTES LONGITUDINALES A-A Y B-B
A-06 CORTES TRANSVERSALES Y ELEVACIONES
A-07 VISTAS EXTERIORES
A-08 VISTAS 3D

LÁMINA
TECHOS, ESTRUCTURA METÁLICA Y DETALLES

ESCALA
INDICADA


FECHA
OCTUBRE 2026

A-04

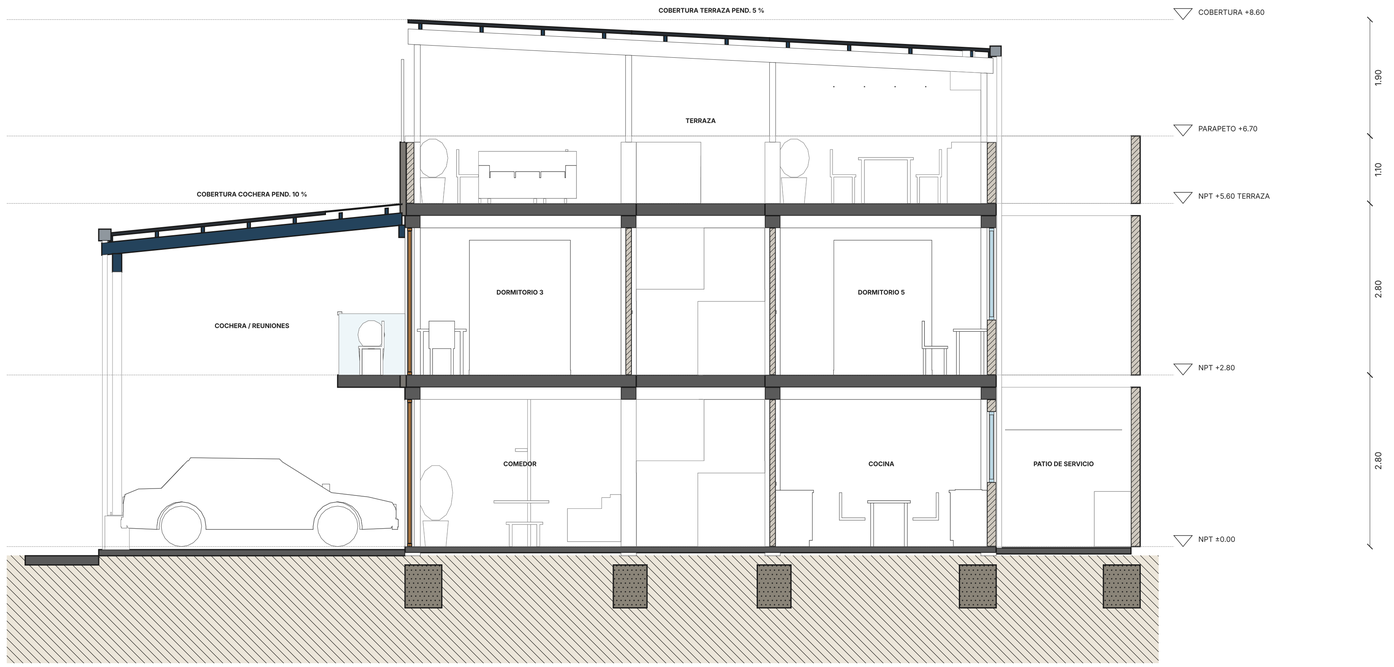

CORTE A-A

ESC. 1/50 · por comedor, hall, cocina y dormitorios 3 y 5 — calle a la izquierda

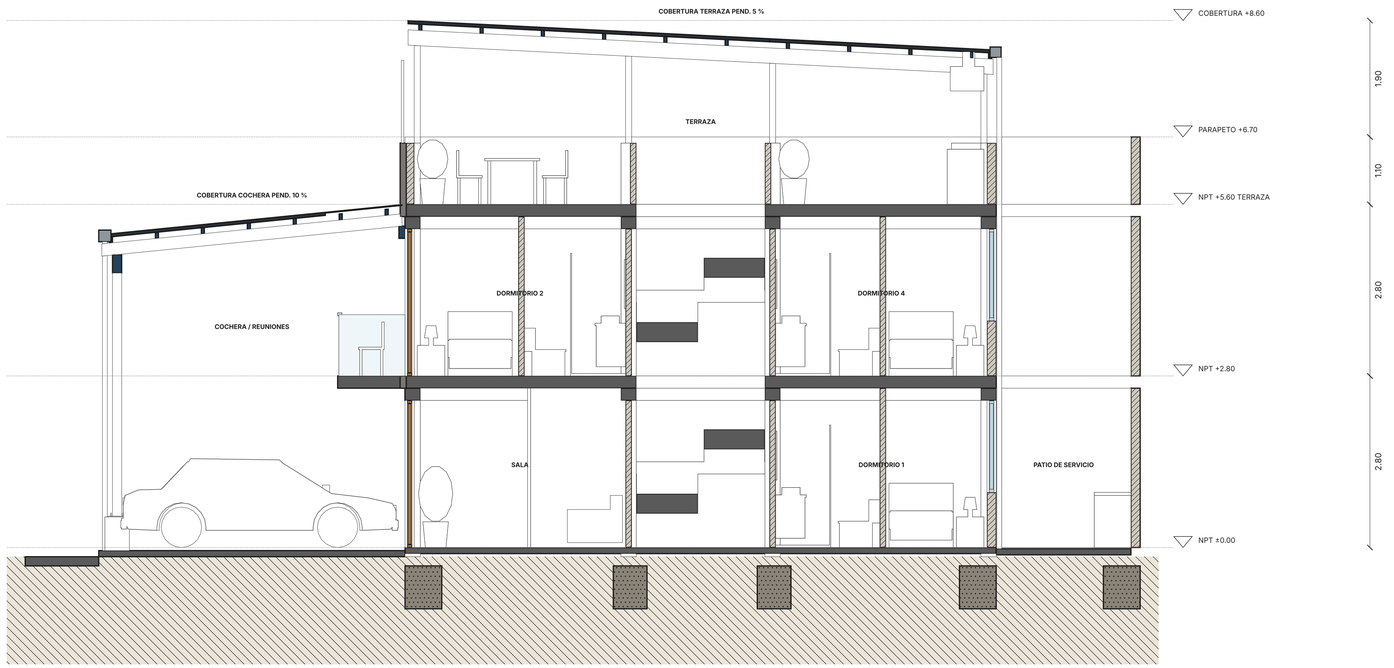

CORTE B-B

ESC. 1/50 · por escalera, sala, dormitorio 1 y dormitorios 2 y 4

CASA LINTERNA

VIVIENDA UNIFAMILIAR · 2 PISOS + TERRAZA + COCHERA TECHADA

TERRENO
8.00 × 17.00 m = 136.00 m²

VIVIENDA
8.00 × 12.00 m · 2 pisos (material noble)

COCHERA
8.00 × 5.00 m · al frente (cob. liviana)

PROPIETARIO
_____

UBICACIÓN
_____

PROYECTISTA
_____

CAP / CIP N°
_____

ESPECIALIDAD
ARQUITECTURA

ÍNDICE DE LÁMINAS


A-01 PLANTA 1er PISO
A-02 PLANTA 2do PISO
A-03 PLANTA DE TERRAZA
A-04 TECHOS, ESTRUCTURA METÁLICA Y DETALLES
A-05 CORTES LONGITUDINALES A-A Y B-B
A-06 CORTES TRANSVERSALES Y ELEVACIONES
A-07 VISTAS EXTERIORES
A-08 VISTAS 3D

LÁMINA
CORTES LONGITUDINALES A-A Y B-B

ESCALA
1/50


FECHA
OCTUBRE 2026

A-05

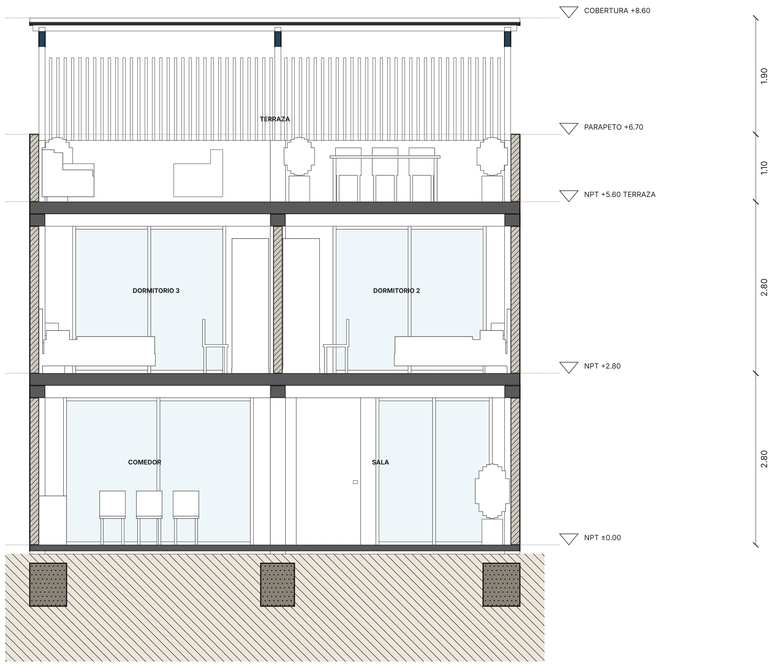

CORTE C-C

ESC. 1/50 · por sala, comedor y dormitorios 2 y 3, mirando a la calle

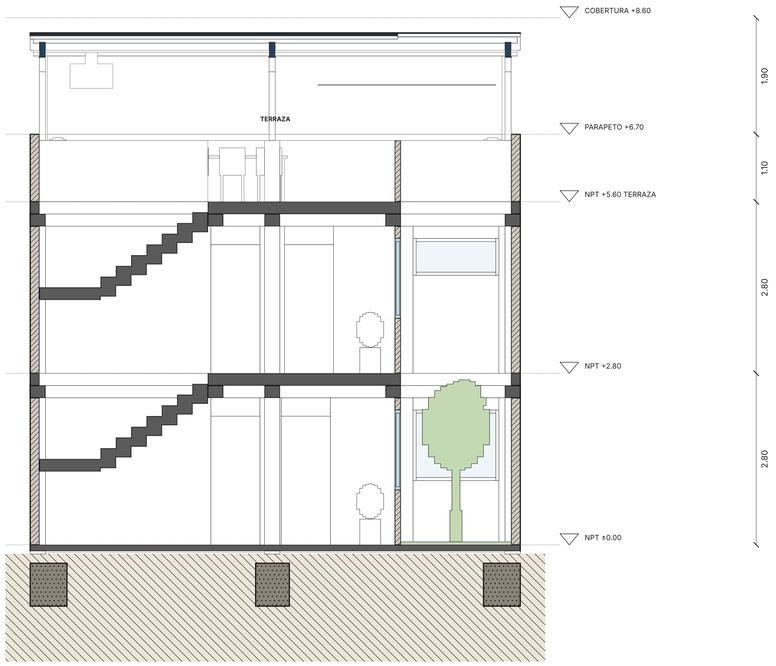


CORTE D-D

ESC. 1/50 · por escalera, hall y pozo de luz, mirando al fondo



ELEVACIÓN PRINCIPAL (CALLE)

ESC. 1/50 · cochera abierta, balcones y celosía de la terraza

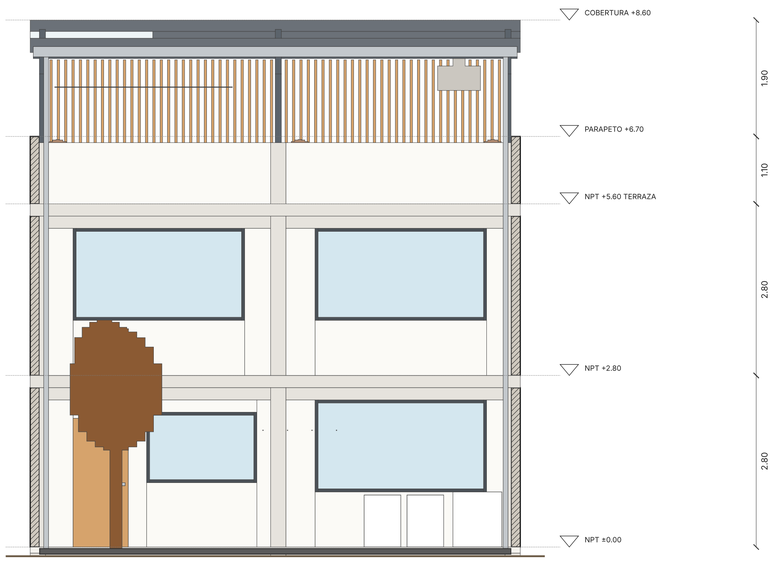

ELEVACIÓN POSTERIOR (PATIO)

ESC. 1/50 · ventanas de dormitorios 1, 4, 5 y cocina

CASA LINTERNA

VIVIENDA UNIFAMILIAR · 2 PISOS + TERRAZA + COCHERA TECHADA

TERRENO
8.00 × 17.00 m = 136.00 m²

VIVIENDA
8.00 × 12.00 m · 2 pisos (material noble)

COCHERA
8.00 × 5.00 m · al frente (cob. liviana)

PROPIETARIO
_____

UBICACIÓN
_____

PROYECTISTA
_____

CAP / CIP N°
_____

ESPECIALIDAD
ARQUITECTURA

ÍNDICE DE LÁMINAS

A-01 PLANTA 1er PISO
A-02 PLANTA 2do PISO
A-03 PLANTA DE TERRAZA
A-04 TECHOS, ESTRUCTURA METÁLICA Y DETALLES
A-05 CORTES LONGITUDINALES A-A Y B-B
A-06 CORTES TRANSVERSALES Y ELEVACIONES
A-07 VISTAS EXTERIORES
A-08 VISTAS 3D

LÁMINA
CORTES TRANSVERSALES Y ELEVACIONES

ESCALA
1/50

FECHA
OCTUBRE 2026

A-06



VISTA DESDE LA CALLE



COCHERA TECHADA BAJO LOS BALCONES

CASA LINTERNA

VIVIENDA UNIFAMILIAR · 2 PISOS + TERRAZA + COCHERA TECHADA

TERRENO
8.00 × 17.00 m = 136.00 m²

VIVIENDA
8.00 × 12.00 m · 2 pisos (material noble)

COCHERA
8.00 × 5.00 m · al frente (cob. liviana)

PROPIETARIO
_____

UBICACIÓN
_____

PROYECTISTA
_____

CAP / CIP N°
_____

ESPECIALIDAD
ARQUITECTURA

ÍNDICE DE LÁMINAS

A-01 PLANTA 1er PISO
A-02 PLANTA 2do PISO
A-03 PLANTA DE TERRAZA
A-04 TECHOS, ESTRUCTURA METÁLICA Y DETALLES
A-05 CORTES LONGITUDINALES A-A Y B-B
A-06 CORTES TRANSVERSALES Y ELEVACIONES
A-07 VISTAS EXTERIORES
A-08 VISTAS 3D

LÁMINA
VISTAS EXTERIORES

ESCALA
S/E

FECHA
OCTUBRE 2026

A-07




ISOMÉTRICA GENERAL



CORTE FUGADO LONGITUDINAL (x = 4.95)



2do PISO — 4 DORMITORIOS CON BAÑO

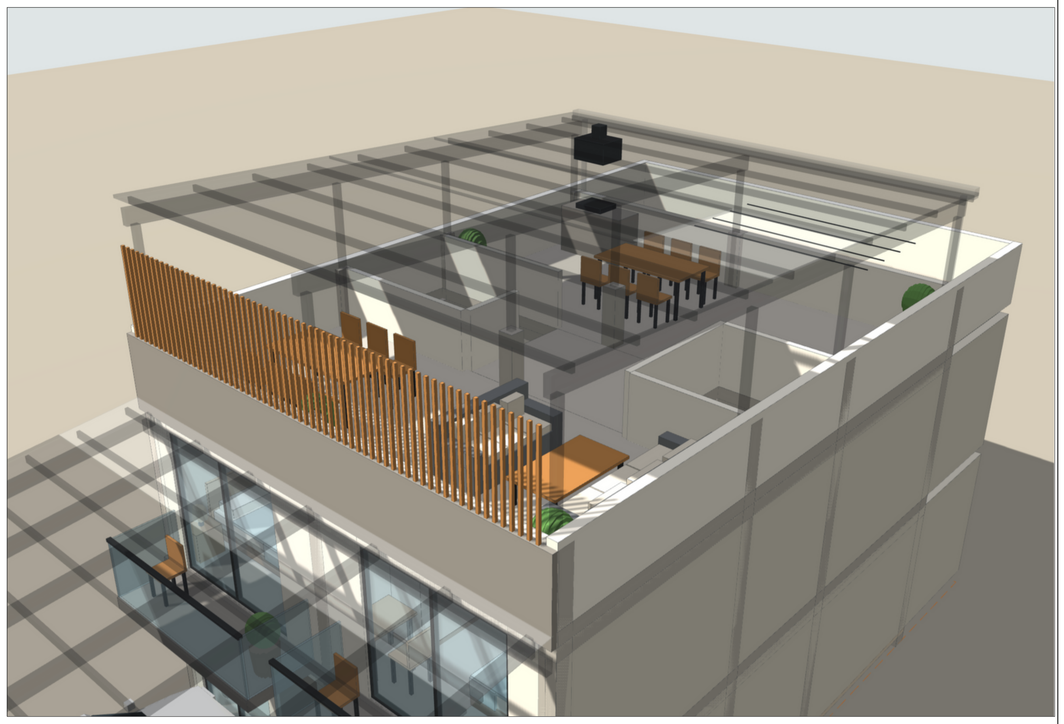

TERRAZA (COBERTURA EN TRANSPARENCIA)

CASA LINTERNA

VIVIENDA UNIFAMILIAR · 2 PISOS + TERRAZA + COCHERA TECHADA

TERRENO
8.00 × 17.00 m = 136.00 m²

VIVIENDA
8.00 × 12.00 m · 2 pisos (material noble)

COCHERA
8.00 × 5.00 m · al frente (cob. liviana)

PROPIETARIO
_____

UBICACIÓN
_____

PROYECTISTA
_____

CAP / CIP N°
_____

ESPECIALIDAD
ARQUITECTURA

ÍNDICE DE LÁMINAS

A-01 PLANTA 1er PISO
A-02 PLANTA 2do PISO
A-03 PLANTA DE TERRAZA
A-04 TECHOS, ESTRUCTURA METÁLICA Y DETALLES
A-05 CORTES LONGITUDINALES A-A Y B-B
A-06 CORTES TRANSVERSALES Y ELEVACIONES
A-07 VISTAS EXTERIORES
A-08 VISTAS 3D

LÁMINA
VISTAS 3D

ESCALA
S/E

FECHA
OCTUBRE 2026

A-08